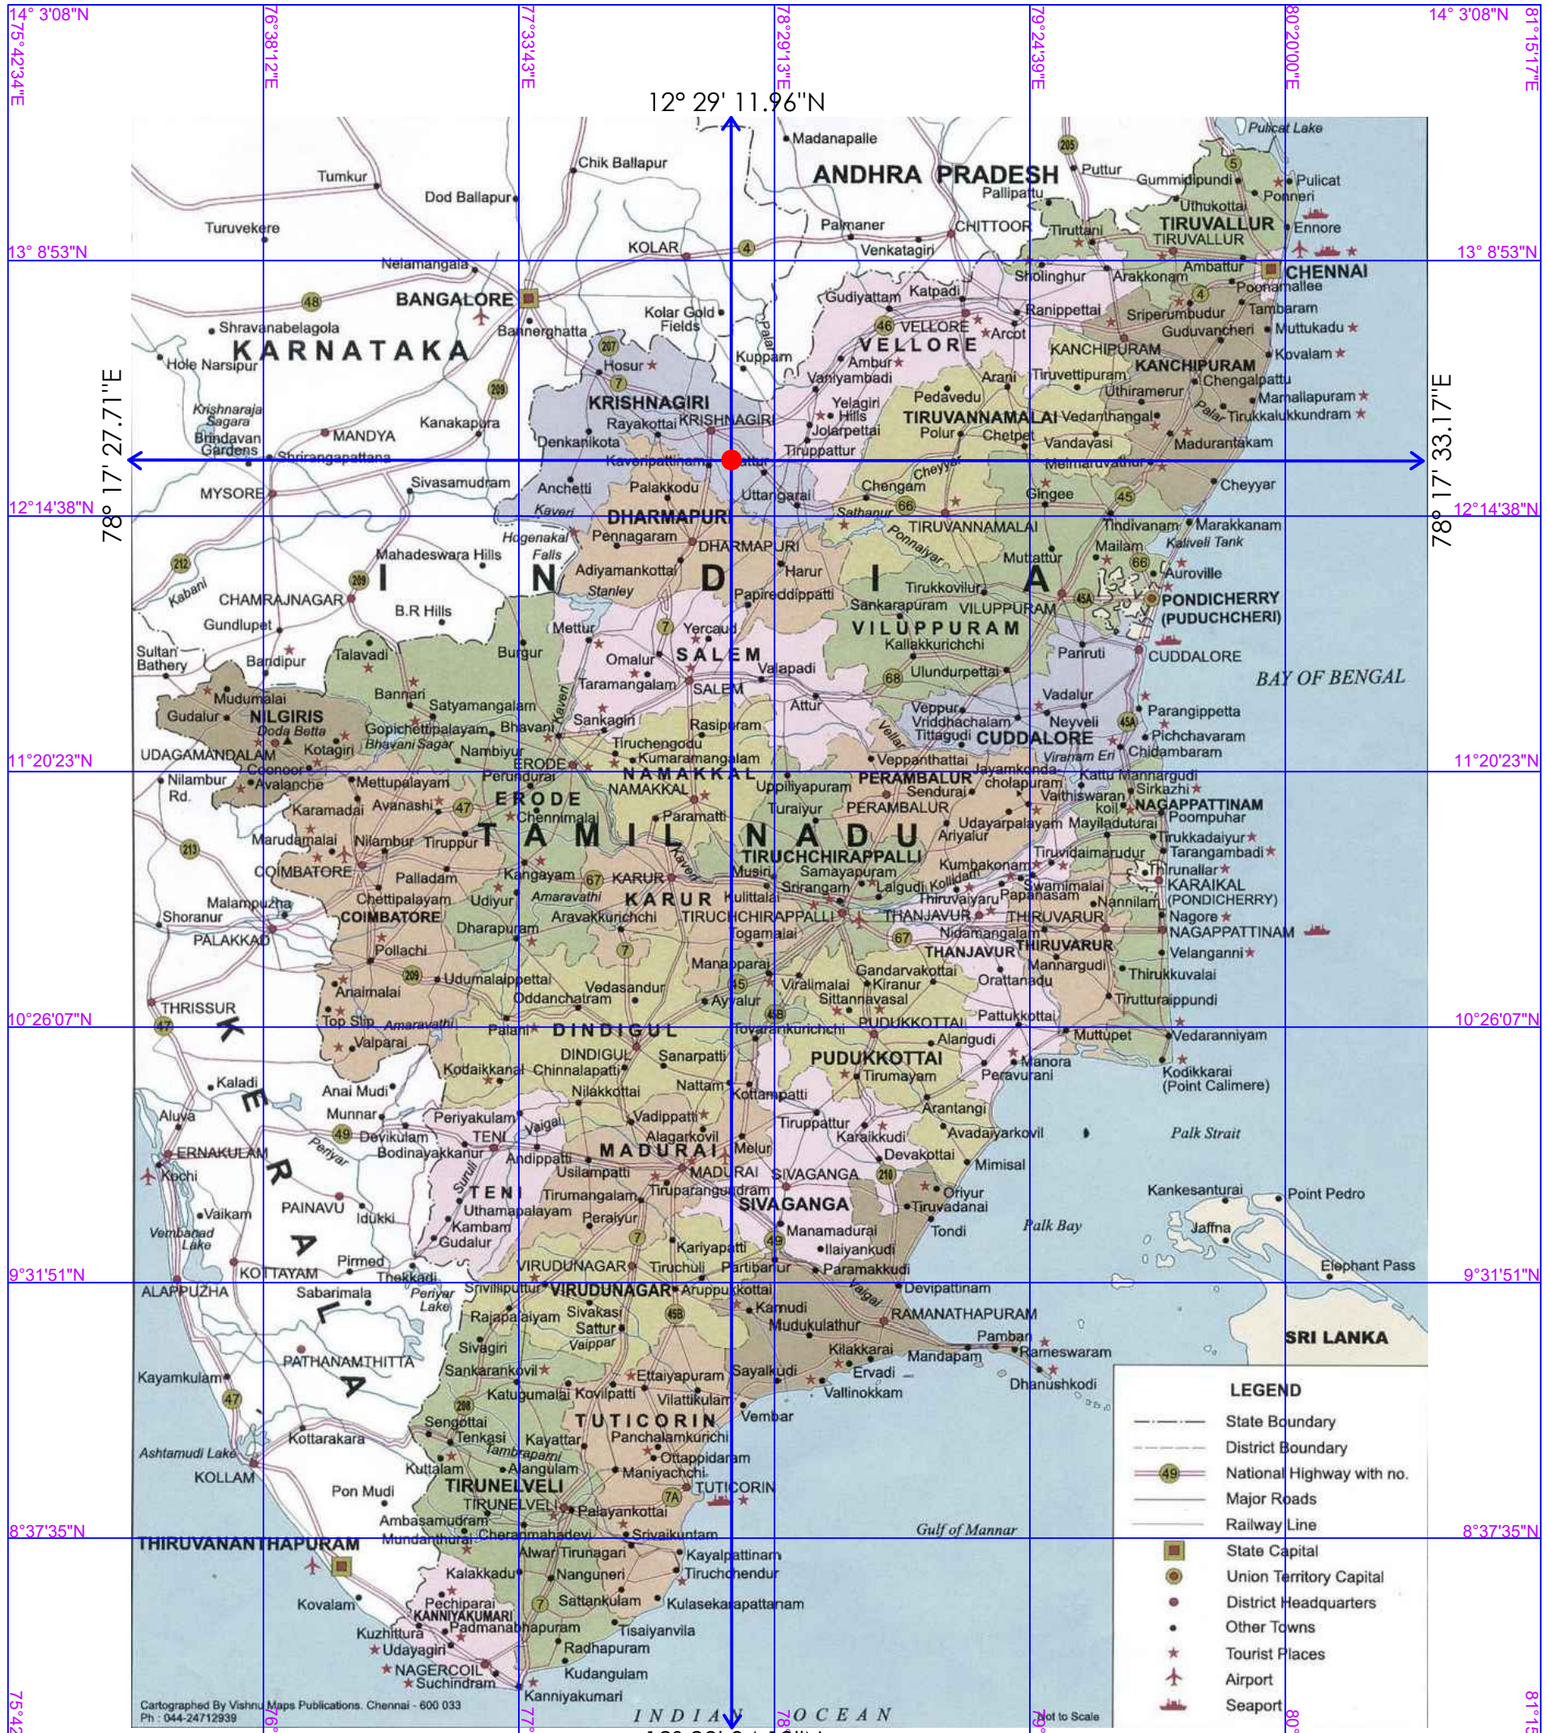


N

PLATE NO:I

DATE OF SURVEY:16.03.2026

APPLICANT:

M/s.AB GRANITE
223/1A,CHENDRAPALLI VILLAGE,
ANCHUR POST,
BARGUR TALUK,
KRISHNAGIRI-635 203.

LOCATION OF QUARRY LEASE APPLIED AREA:

SF.NOS	:223/1A1(P)&224/2A(P),
EXTENT	:1.80.00 HA,
VILLAGE	:CHENDRAPALLI,
TALUK	:BARGUR,
DISTRICT	:KRISHNAGIRII,
STATE	:TAMILNADU.

INDEX

Q. L.A. AREA :

TOPO SHEET NO. : 57 L/07

LATITUDE : 12° 29' 04.19''N to 12° 29' 11.96''N

LONGITUDE : 78° 17' 27.71''E to 78° 17' 33.17''E

LOCATION PLAN


SCALE 1:24,00,000

PREPARED BY :

THIS IS TO CERTIFY THAT THE INFORMATION IN THIS PLATE IS TRUE AND CORRECT TO THE BEST OF MY KNOWLEDGE BASED UPON THE LEASEMAP AUTHENTICATED BY STATE GOVERNMENT

B.VENGADAGIRI,M.Sc.,
QUALIFIED PERSON
Under Rule 15(I)(a)and(b)of MCR,2016

12° 34' 37.14"N

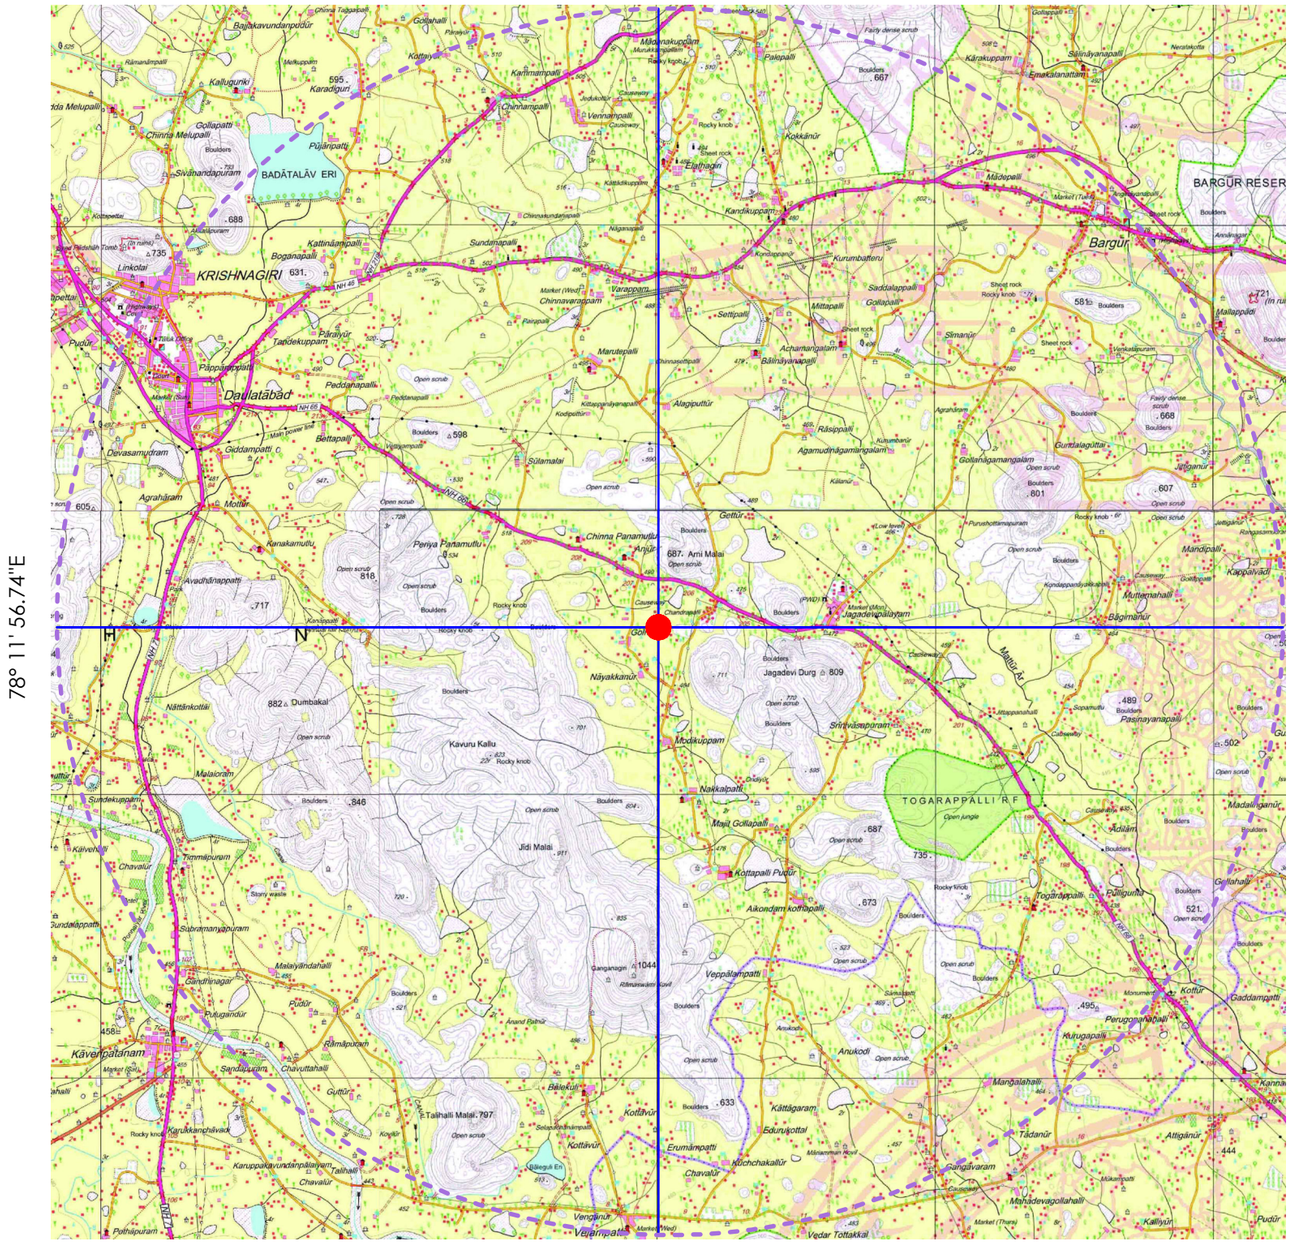

12° 23' 39.01"N

TOPO SHEET NO. : 57 L/07	
LATITUDE : 12° 29' 04.19"N to 12° 29' 11.96"N	
LONGITUDE : 78° 17' 27.71"E to 78° 17' 33.17"E	
10KM RADIUS :	
Q.L.APPLIED AREA :	

PLATE NO:I-A

DATE OF SURVEY:16.03.2026


APPLICANT:

M/s.AB GRANITE
223/1A,CHENDRAPALLI VILLAGE,
ANCHUR POST,
BARGUR TALUK,
KRISHNAGIRI-635 203.

LOCATION OF QUARRY LEASE APPLIED AREA:

SF.NOS	:223/1A1(P)&224/2A(P),
EXTENT	:1.80.00 HA,
VILLAGE	:CHENDRAPALLI,
TALUK	:BARGUR,
DISTRICT	:KRISHNAGIRII,
STATE	:TAMILNADU.

INDEX

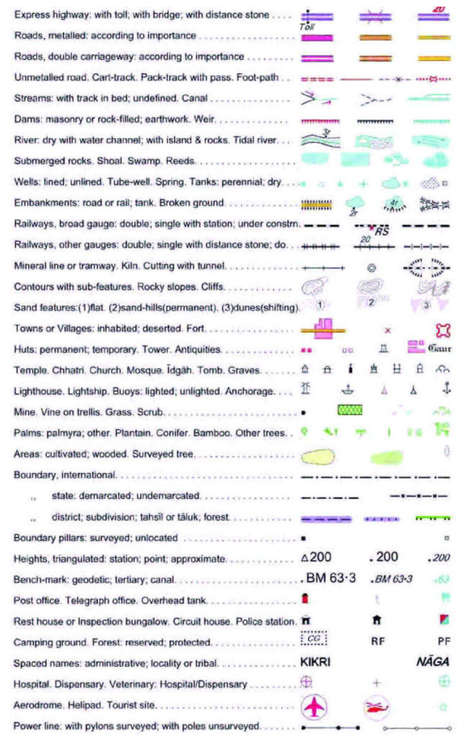


TOPO SKETCH OF QUARRY LEASE APPLIED AREA FOR 10Km RADIUS

SCALE– 1:100000

PREPARED BY :

THIS IS TO CERTIFY THAT THE INFORMATION IN THIS PLATE IS TRUE AND CORRECT TO THE BEST OF MY KNOWLEDGE BASED UPON THE LEASE MAP AUTHENTICATED BY STATE GOVERNMENT

B.VENGADAGIRI,M.Sc.,
QUALIFIED PERSON
Under Rule 15(I)(a)and(b)of MCR,2016

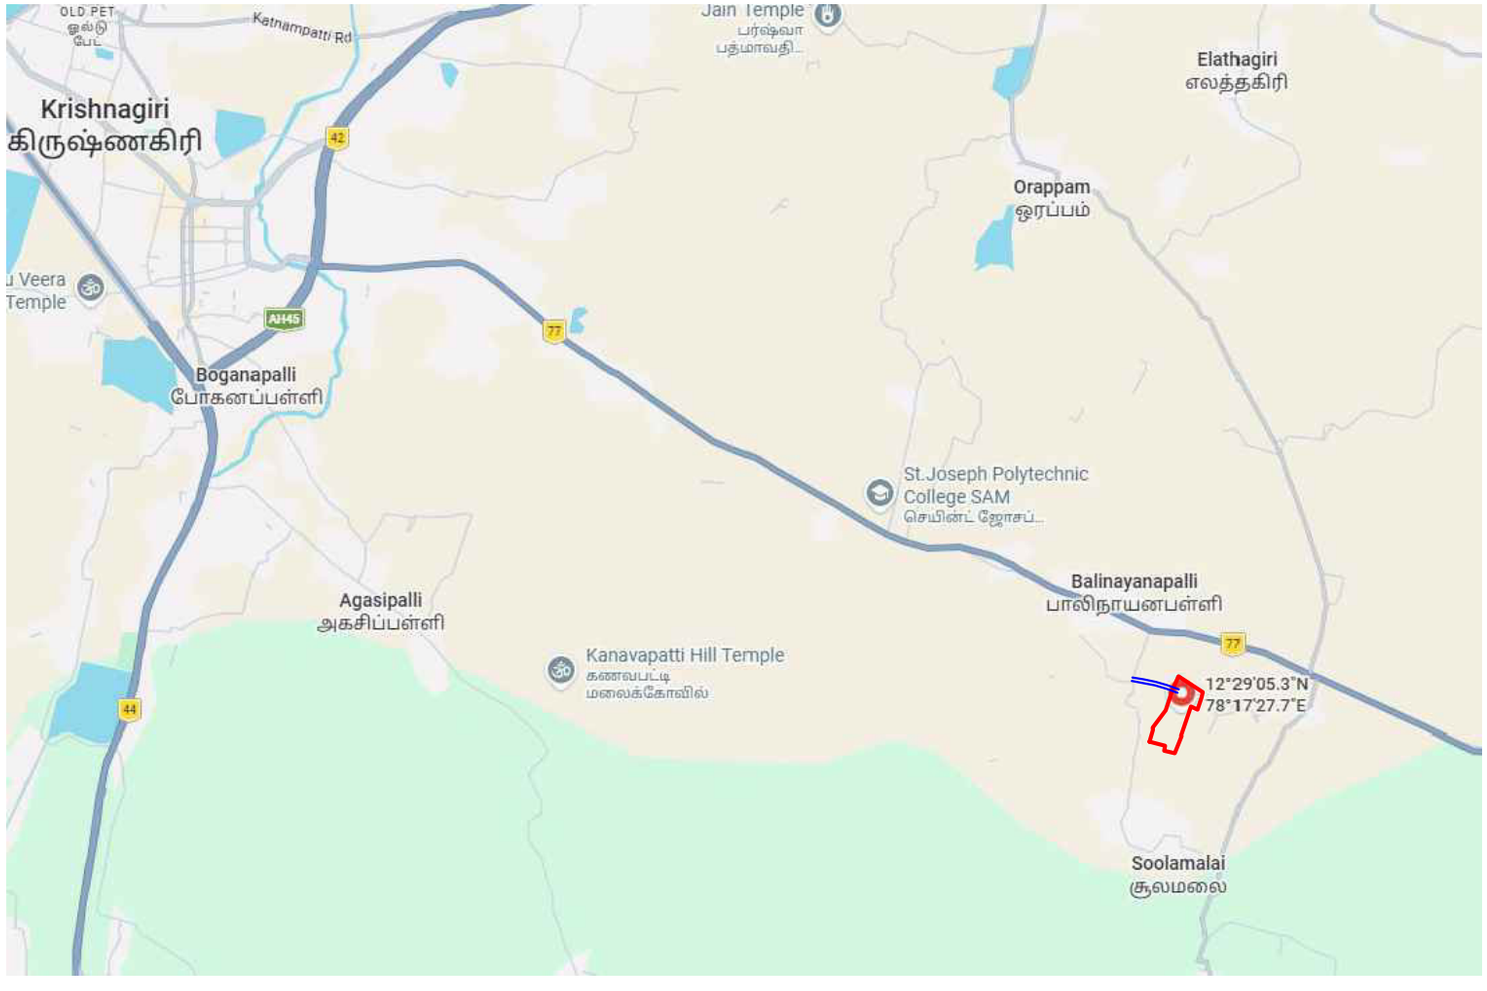

N

PLATE NO: I-B

DATE OF SURVEY:16.03.2026

APPLICANT:

M/s.AB GRANITE
223/1A,CHENDRAPALLI VILLAGE,
ANCHUR POST,
BARGUR TALUK,
KRISHNAGIRI-635 203.

LOCATION OF QUARRY LEASE APPLIED AREA:

SF.NOS	:223/1A1(P)&224/2A(P),
EXTENT	:1.80.00 HA,
VILLAGE	:CHENDRAPALLI,
TALUK	:BARGUR,
DISTRICT	:KRISHNAGIRII,
STATE	:TAMILNADU.

INDEX

Q.L.APPLIED AREA

APPROACH ROAD

VILLAGE ROAD

NATIONAL HIGHWAY


ROUTE MAP

Not To Scale

PREPARED BY :

THIS IS TO CERTIFY THAT THE INFORMATION IN THIS PLATE IS TRUE AND CORRECT TO THE BEST OF MY KNOWLEDGE BASED UPON THE LEASE MAP AUTHENTICATED BY STATE GOVERNMENT

B.VENGADAGIRI,M.Sc.,
QUALIFIED PERSON
Under Rule 15(I)(a)and(b)of MCR,2016

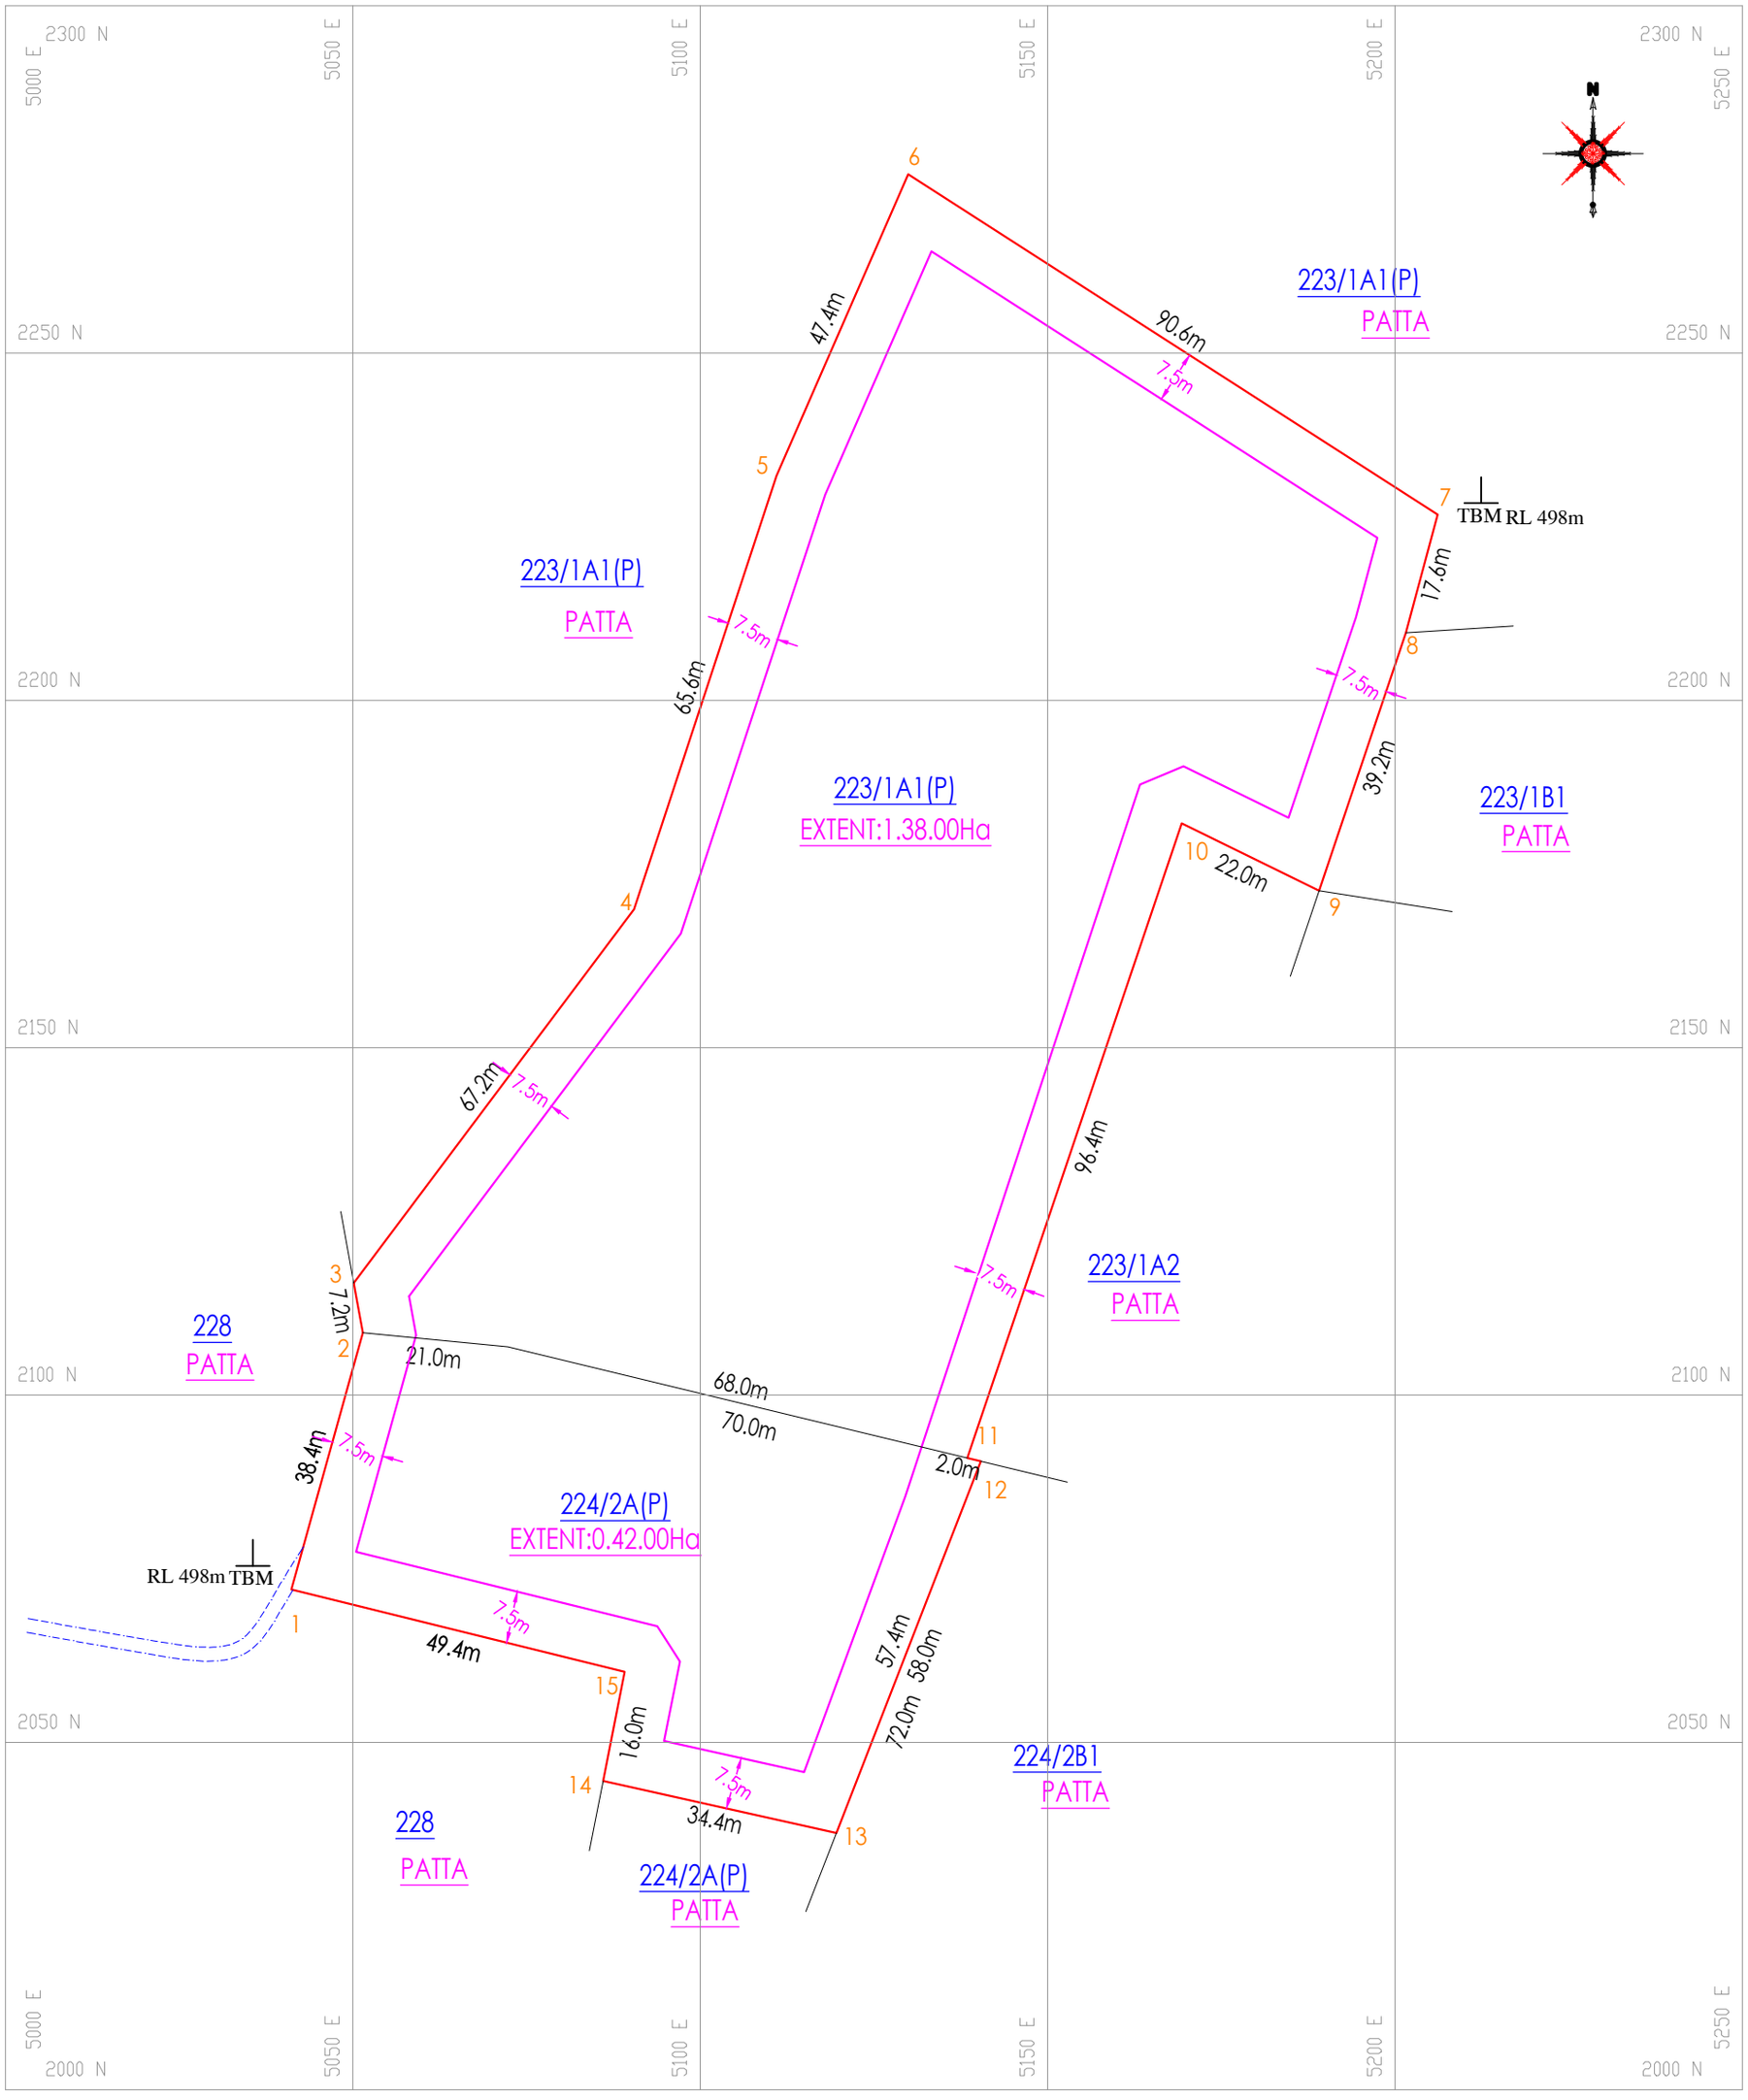

BOUNDARY CO-ORDINATES

S.N.	LATITUDE	LONGITUDE
1	12° 29' 05.33"N	78° 17' 27.71"E
2	12° 29' 06.53"N	78° 17' 28.05"E
3	12° 29' 06.76"N	78° 17' 28.01"E
4	12° 29' 08.51"N	78° 17' 29.34"E
5	12° 29' 10.54"N	78° 17' 30.02"E
6	12° 29' 11.96"N	78° 17' 30.64"E
7	12° 29' 10.37"N	78° 17' 33.17"E
8	12° 29' 09.81"N	78° 17' 33.01"E
9	12° 29' 08.61"N	78° 17' 32.60"E
10	12° 29' 08.92"N	78° 17' 31.95"E
11	12° 29' 05.95"N	78° 17' 30.93"E
12	12° 29' 05.93"N	78° 17' 31.00"E
13	12° 29' 04.19"N	78° 17' 30.31"E
14	12° 29' 04.43"N	78° 17' 29.20"E
15	12° 29' 04.94"N	78° 17' 29.30"E

DATUM : UTM-WGS84, ZONE 44 NORTH

PLATE NO.II

DATE OF SURVEY:16.03.2026

APPLICANT:

M/s.AB GRANITE
223/1A,CHENDRAPALLI VILLAGE,
ANCHUR POST,
BARGUR TALUK,
KRISHNAGIRI-635 203.

LOCATION OF QUARRY LEASE APPLIED AREA:

SF.NOS :223/1A1(P)&224/2A(P),
EXTENT :1.80.00 HA,
VILLAGE :CHENDRAPALLI,
TALUK :BARGUR,
DISTRICT :KRISHNAGIRII,
STATE :TAMILNADU.

INDEX

- Q.L.APPLIED AREA BOUNDARY
- 7.5m SAFETY DISTANCE
- APPROACH ROAD
- TEMPORARY BENCH MARK (TBM)

QUARRY LEASE PLAN

SCALE 1:1000

PREPARED BY:

THIS IS TO CERTIFY THAT THE INFORMATION IN THIS PLATE IS TRUE AND CORRECT TO THE BEST OF MY KNOWLEDGE BASED UPON THE LEASEMAP AUTHENTICATED BY STATE GOVERNMENT

B.VENGADAGIRI,M.Sc.,
QUALIFIED PERSON
Under Rule 15(I)(a)and(b)of MCR,2016

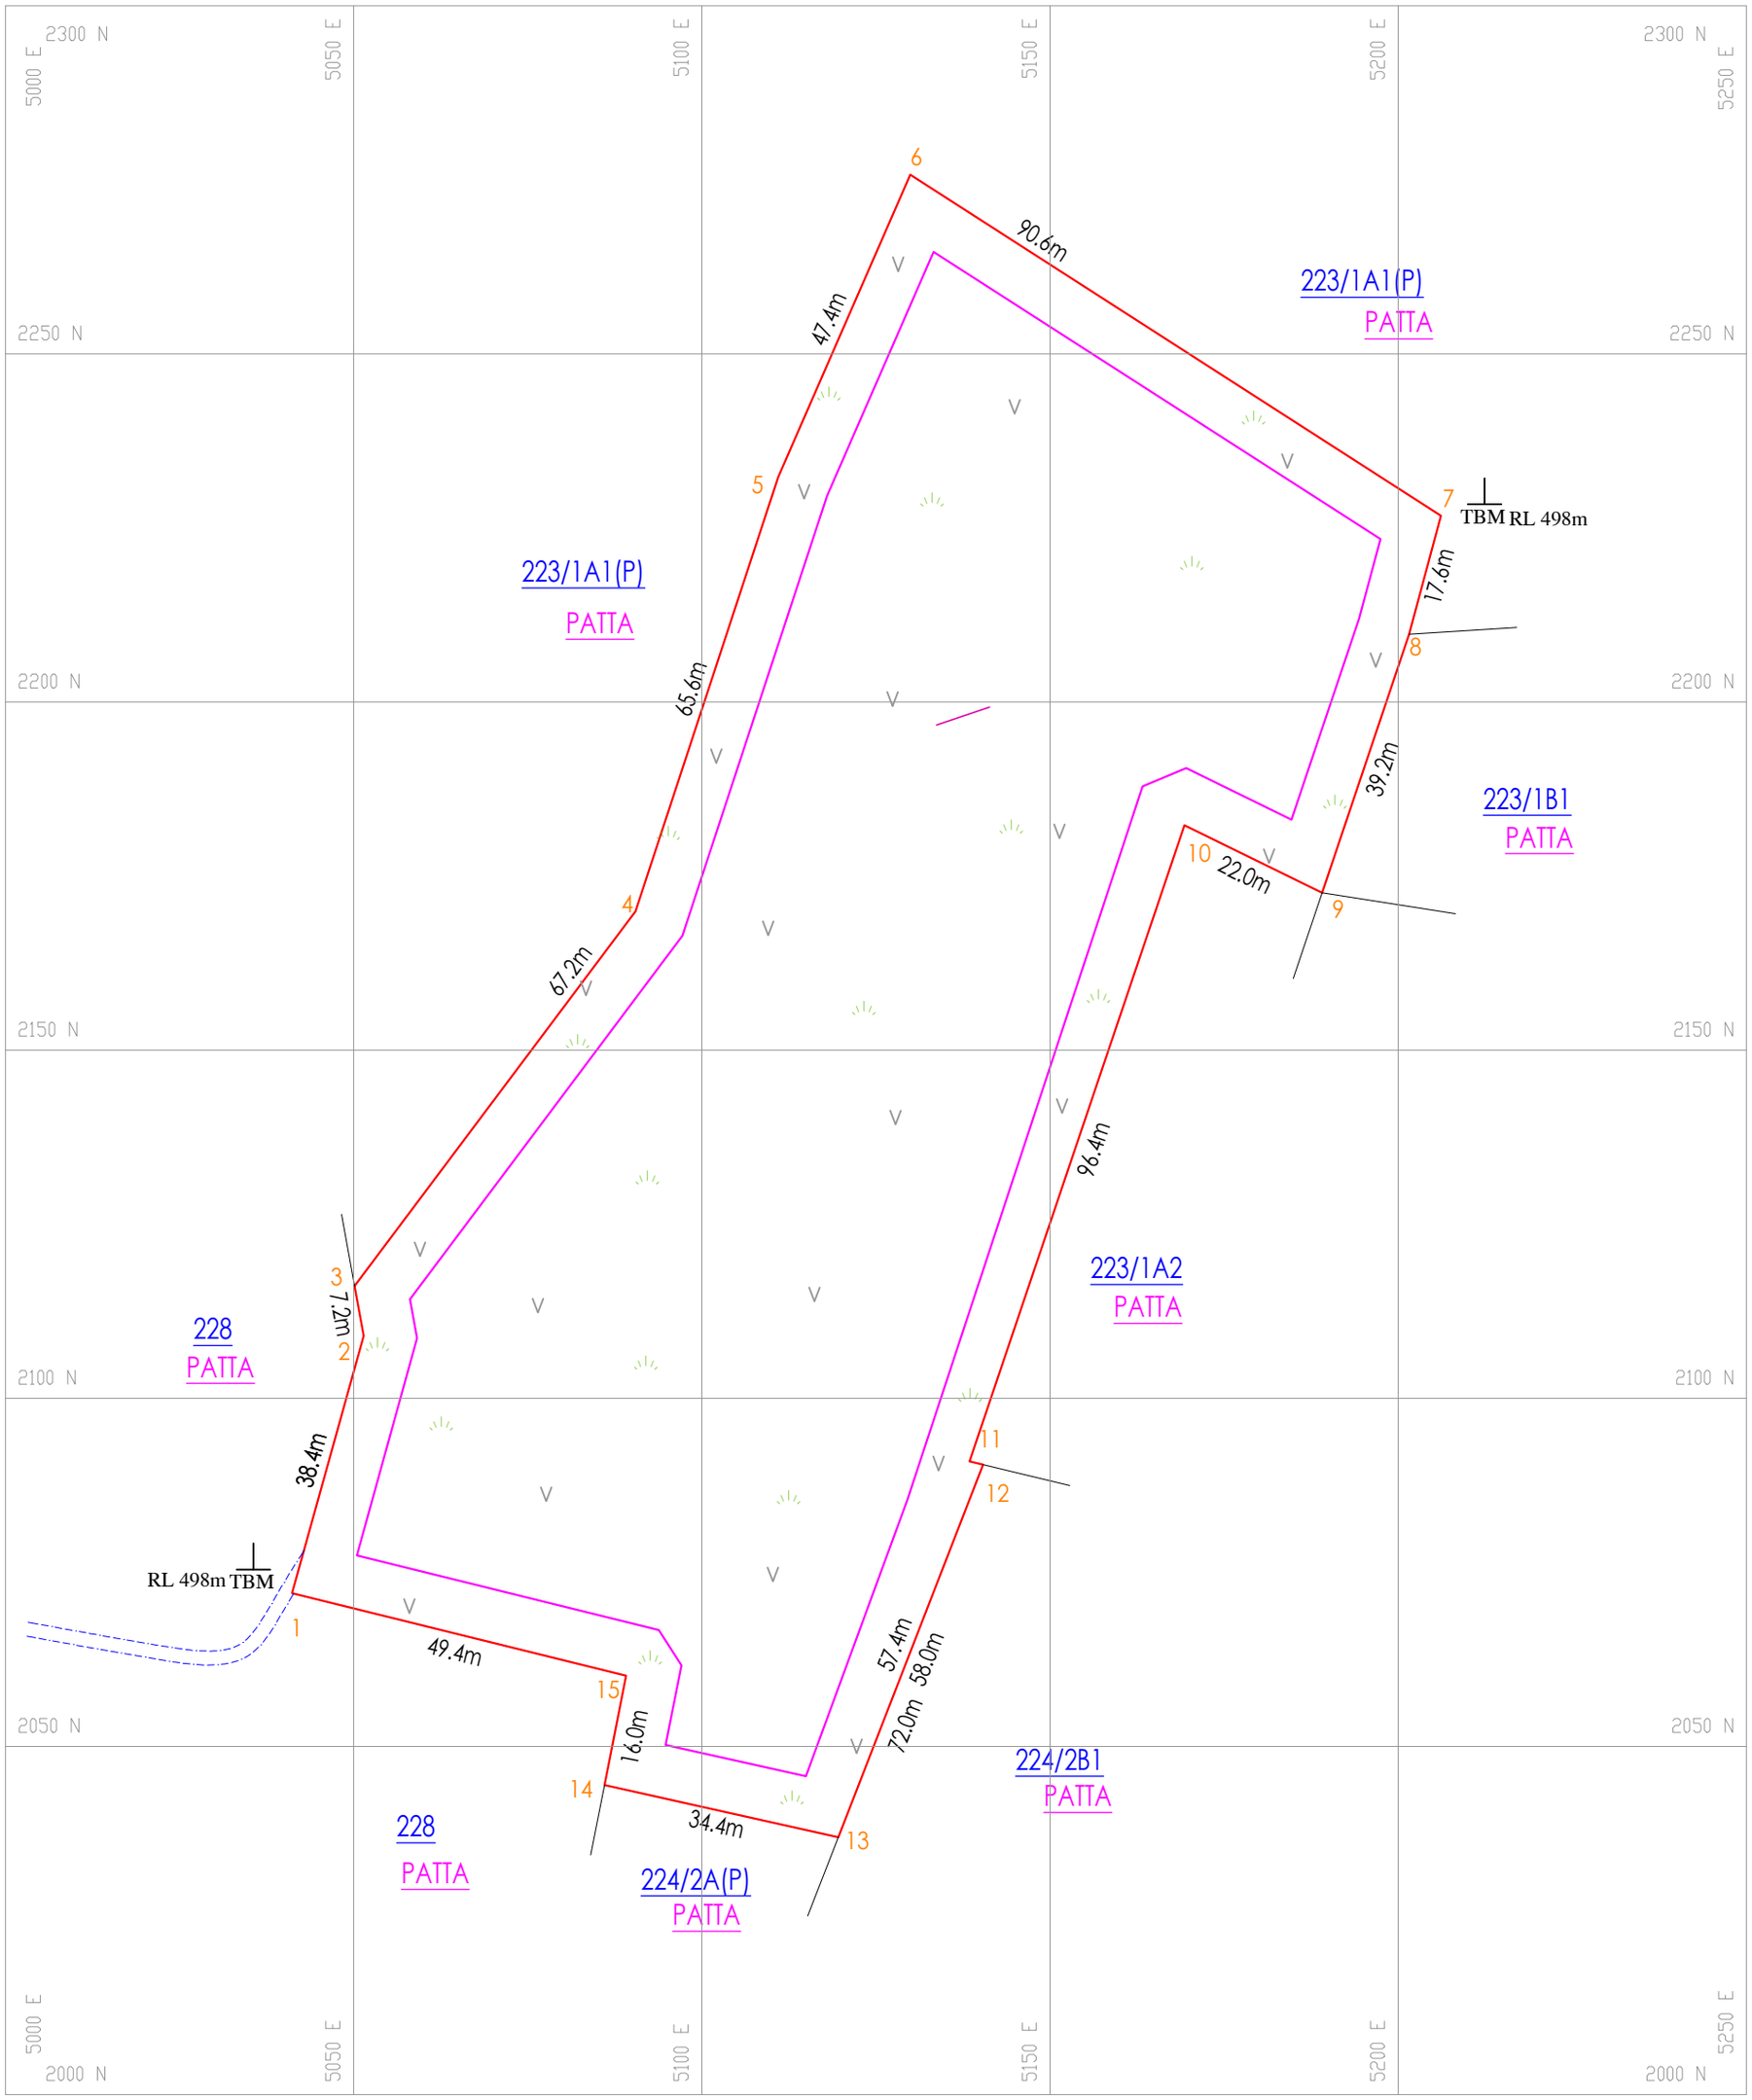


PLATE NO.III

DATE OF SURVEY:16.03.2026

APPLICANT:

M/s.AB GRANITE
223/1A,CHENDRAPALLI VILLAGE,
ANCHUR POST,
BARGUR TALUK,
KRISHNAGIRI-635 203.

LOCATION OF QUARRY LEASE APPLIED AREA:

SF.NOS :223/1A1(P)&224/2A(P),
EXTENT :1.80.00 HA,
VILLAGE :CHENDRAPALLI,
TALUK :BARGUR,
DISTRICT :KRISHNAGIRII,
STATE :TAMILNADU.

INDEX

- Q.L.APPLIED AREA BOUNDARY
- 7.5m SAFETY DISTANCE
- TEMPORARY BENCH MARK (TBM)
- TOP SOIL (V V V)
- SCRUB
- APPROACH ROAD


SURFACE PLAN

SCALE 1:1000


PREPARED BY:

THIS IS TO CERTIFY THAT THE INFORMATION IN THIS PLATE IS TRUE AND CORRECT TO THE BEST OF MY KNOWLEDGE BASED UPON THE LEASEMAP AUTHENTICATED BY STATE GOVERNMENT


B.VENGADAGIRI,M.Sc.,
QUALIFIED PERSON
Under Rule 15(I)(a)and(b)of MCR,2016

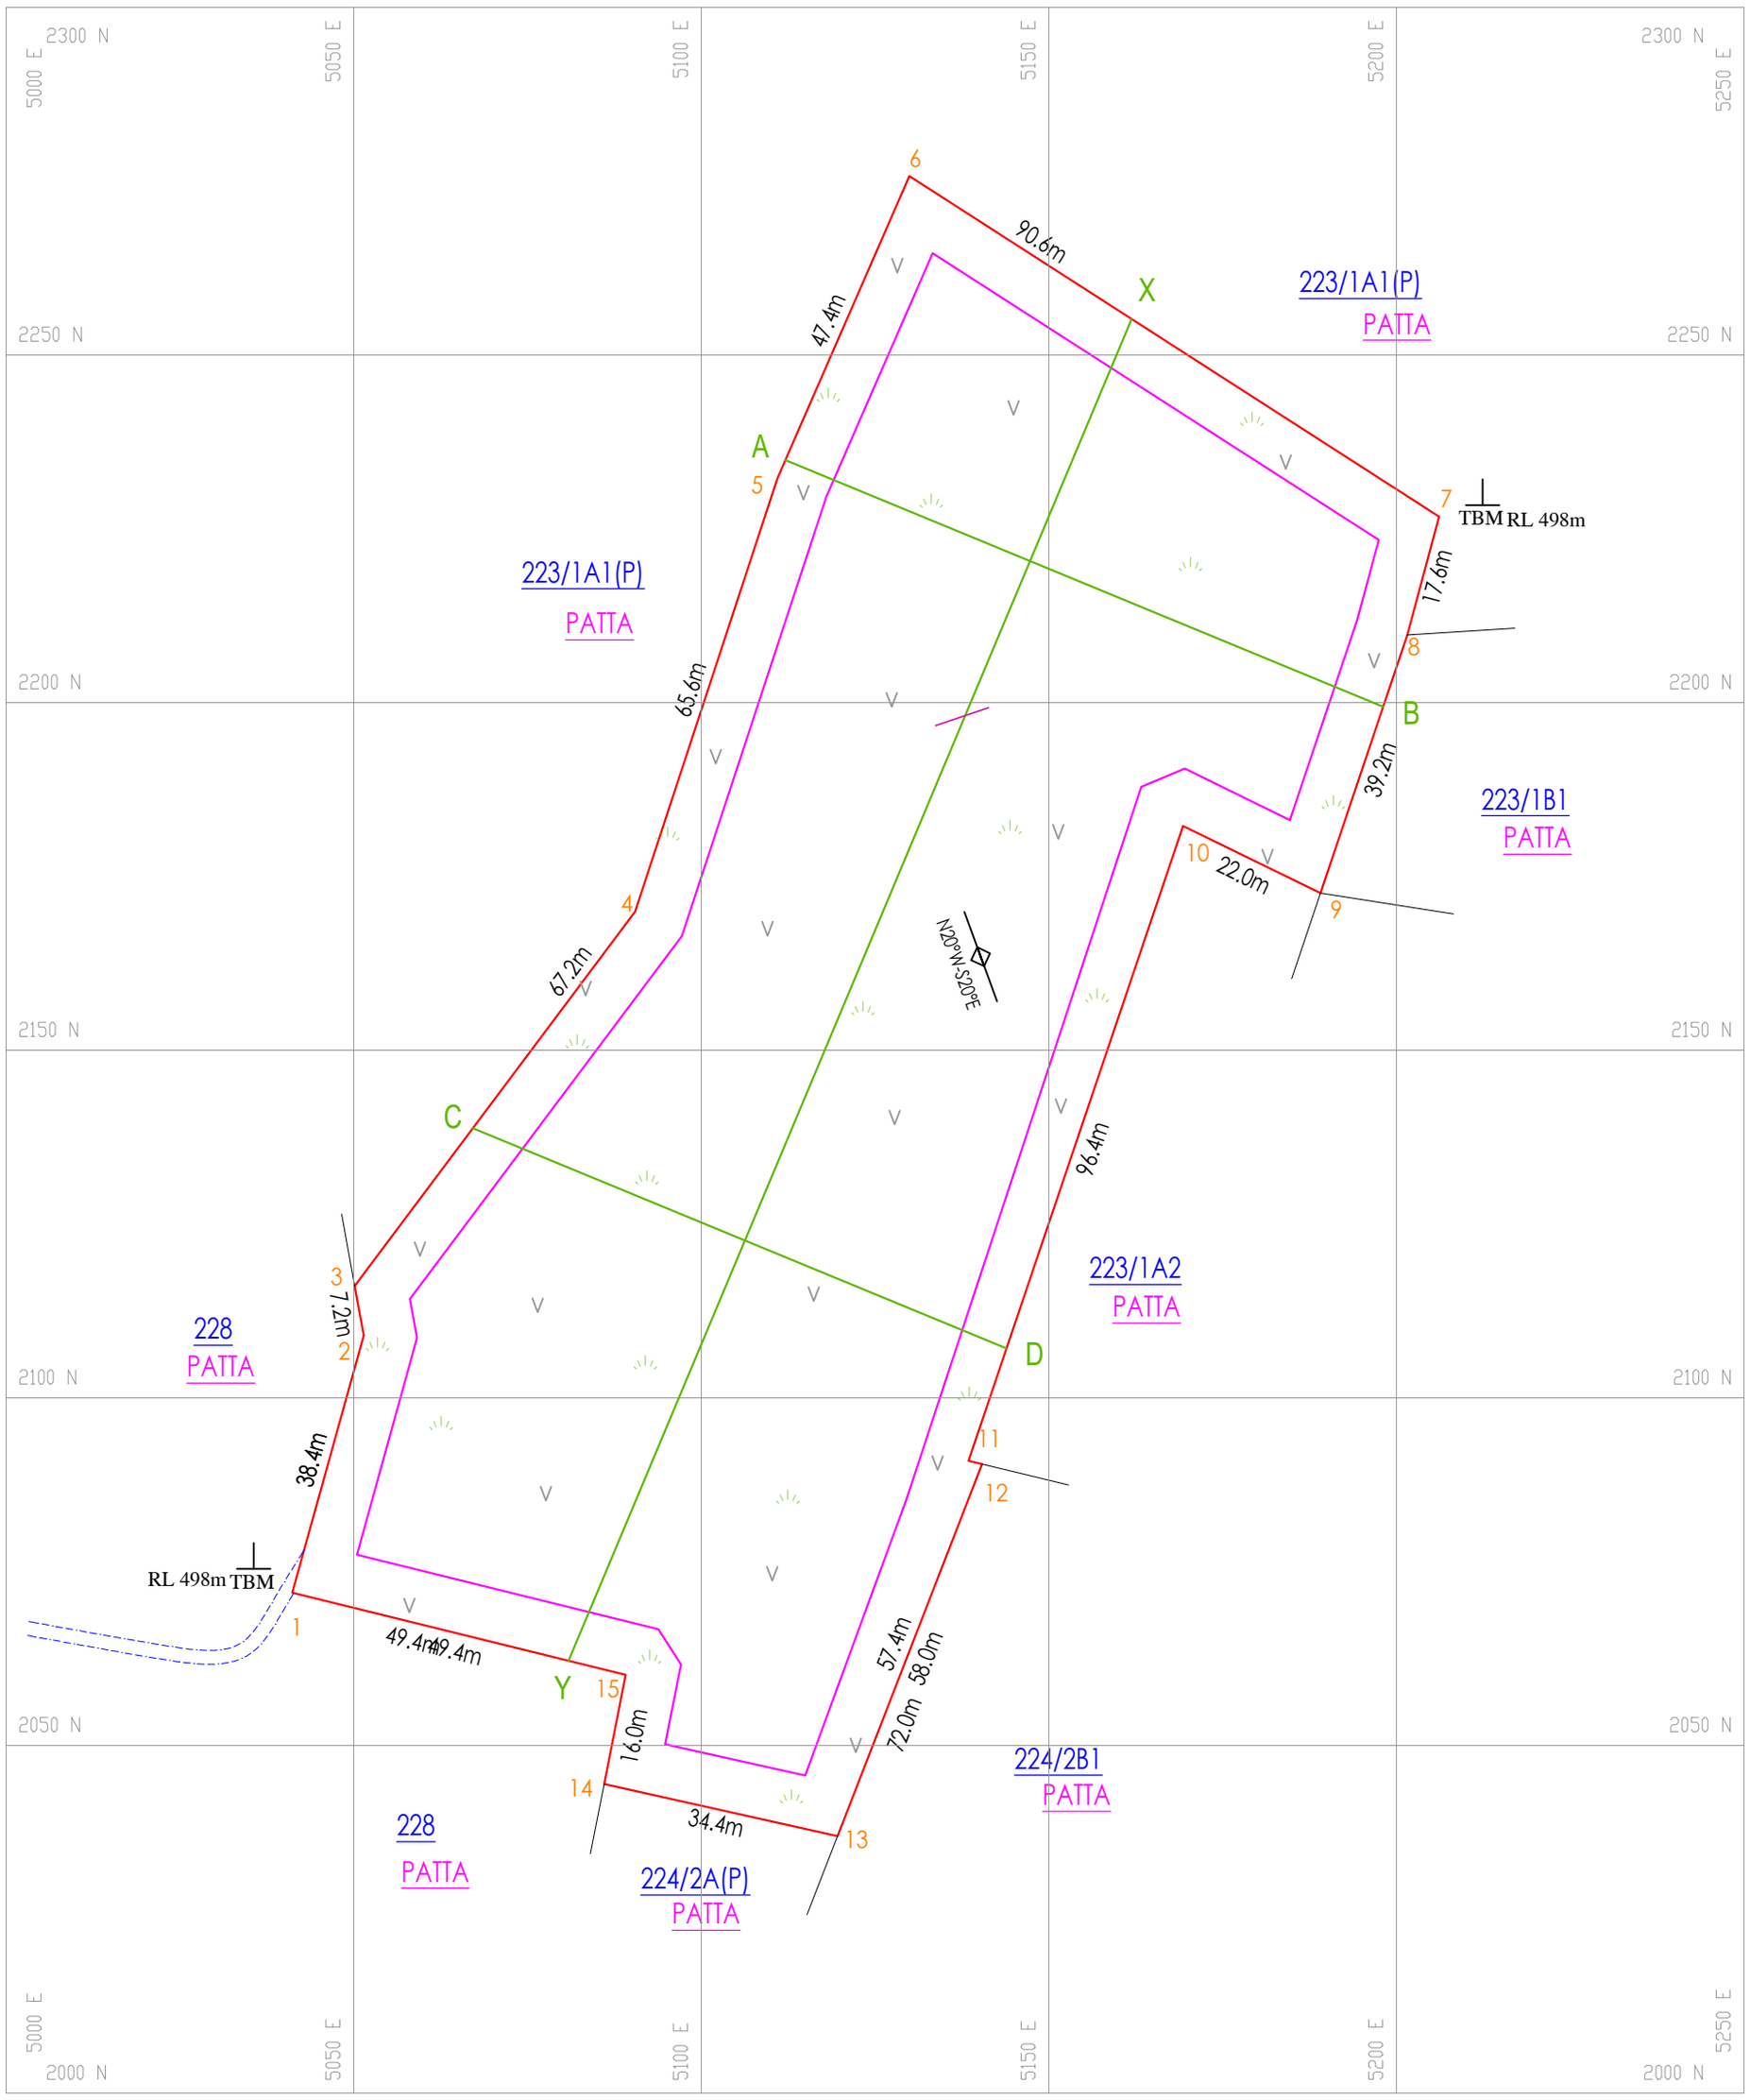

SECTION ALONG X–Y

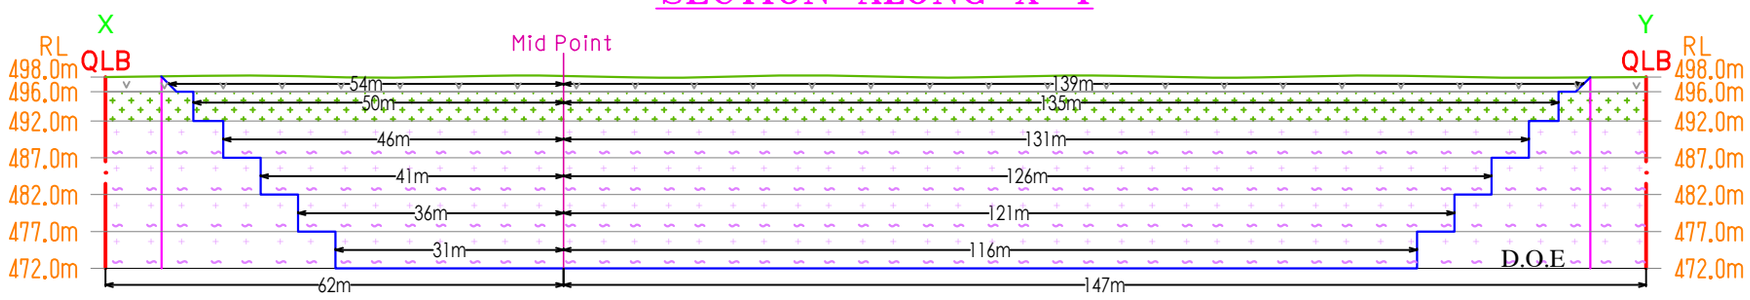

SECTION ALONG A–B

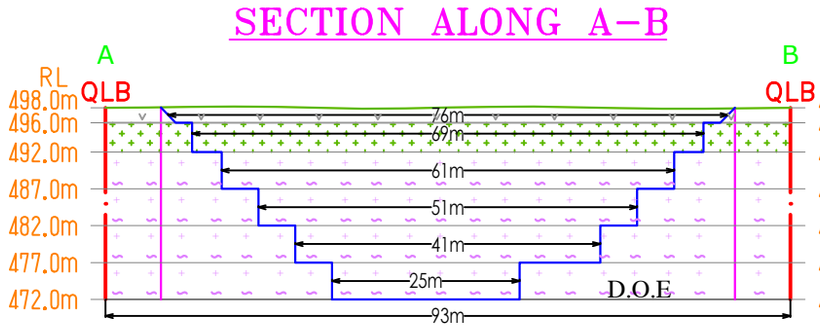

SECTION ALONG C–D

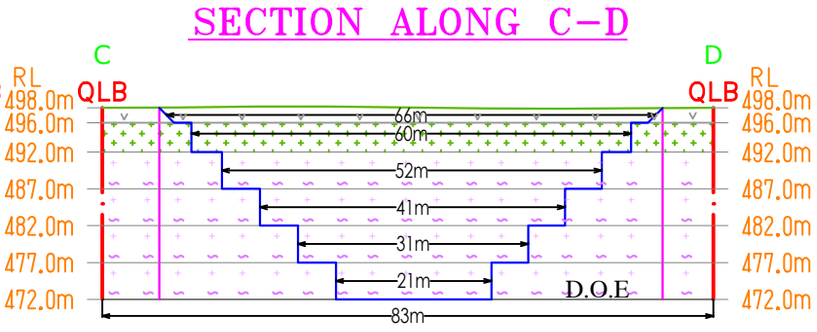


PLATE NO.IV

DATE OF SURVEY:16.03.2026

APPLICANT:

M/s.AB GRANITE
223/1A,CHENDRAPALLI VILLAGE,
ANCHUR POST,
BARGUR TALUK,
KRISHNAGIRI-635 203.

LOCATION OF QUARRY LEASE APPLIED AREA:

SF.NOS :223/1A1(P)&224/2A(P),
EXTENT :1.80.00 HA,
VILLAGE :CHENDRAPALLI,
TALUK :BARGUR,
DISTRICT :KRISHNAGIRII,
STATE :TAMILNADU.

INDEX

- Q.L.APPLIED AREA BOUNDARY
- 7.5m SAFETY DISTANCE
- TEMPORARY BENCH MARK (TBM)
- TOP SOIL (V V V)
- WEATHERED ROCK
- STRIKE AND DIP
- GREY GRANITE
- SCRUB
- APPROACH ROAD
- DEPTH OF ESTIMATION (D.O.E)


GEOLOGICAL PLAN & SECTIONS

SCALE 1:1000


PREPARED BY:

THIS IS TO CERTIFY THAT THE INFORMATION IN THIS PLATE IS TRUE AND CORRECT TO THE BEST OF MY KNOWLEDGE BASED UPON THE LEASEMAP AUTHENTICATED BY STATE GOVERNMENT


B.VENGADAGIRI,M.Sc.,
QUALIFIED PERSON
Under Rule 15(I)(a)and(b)of MCR,2016

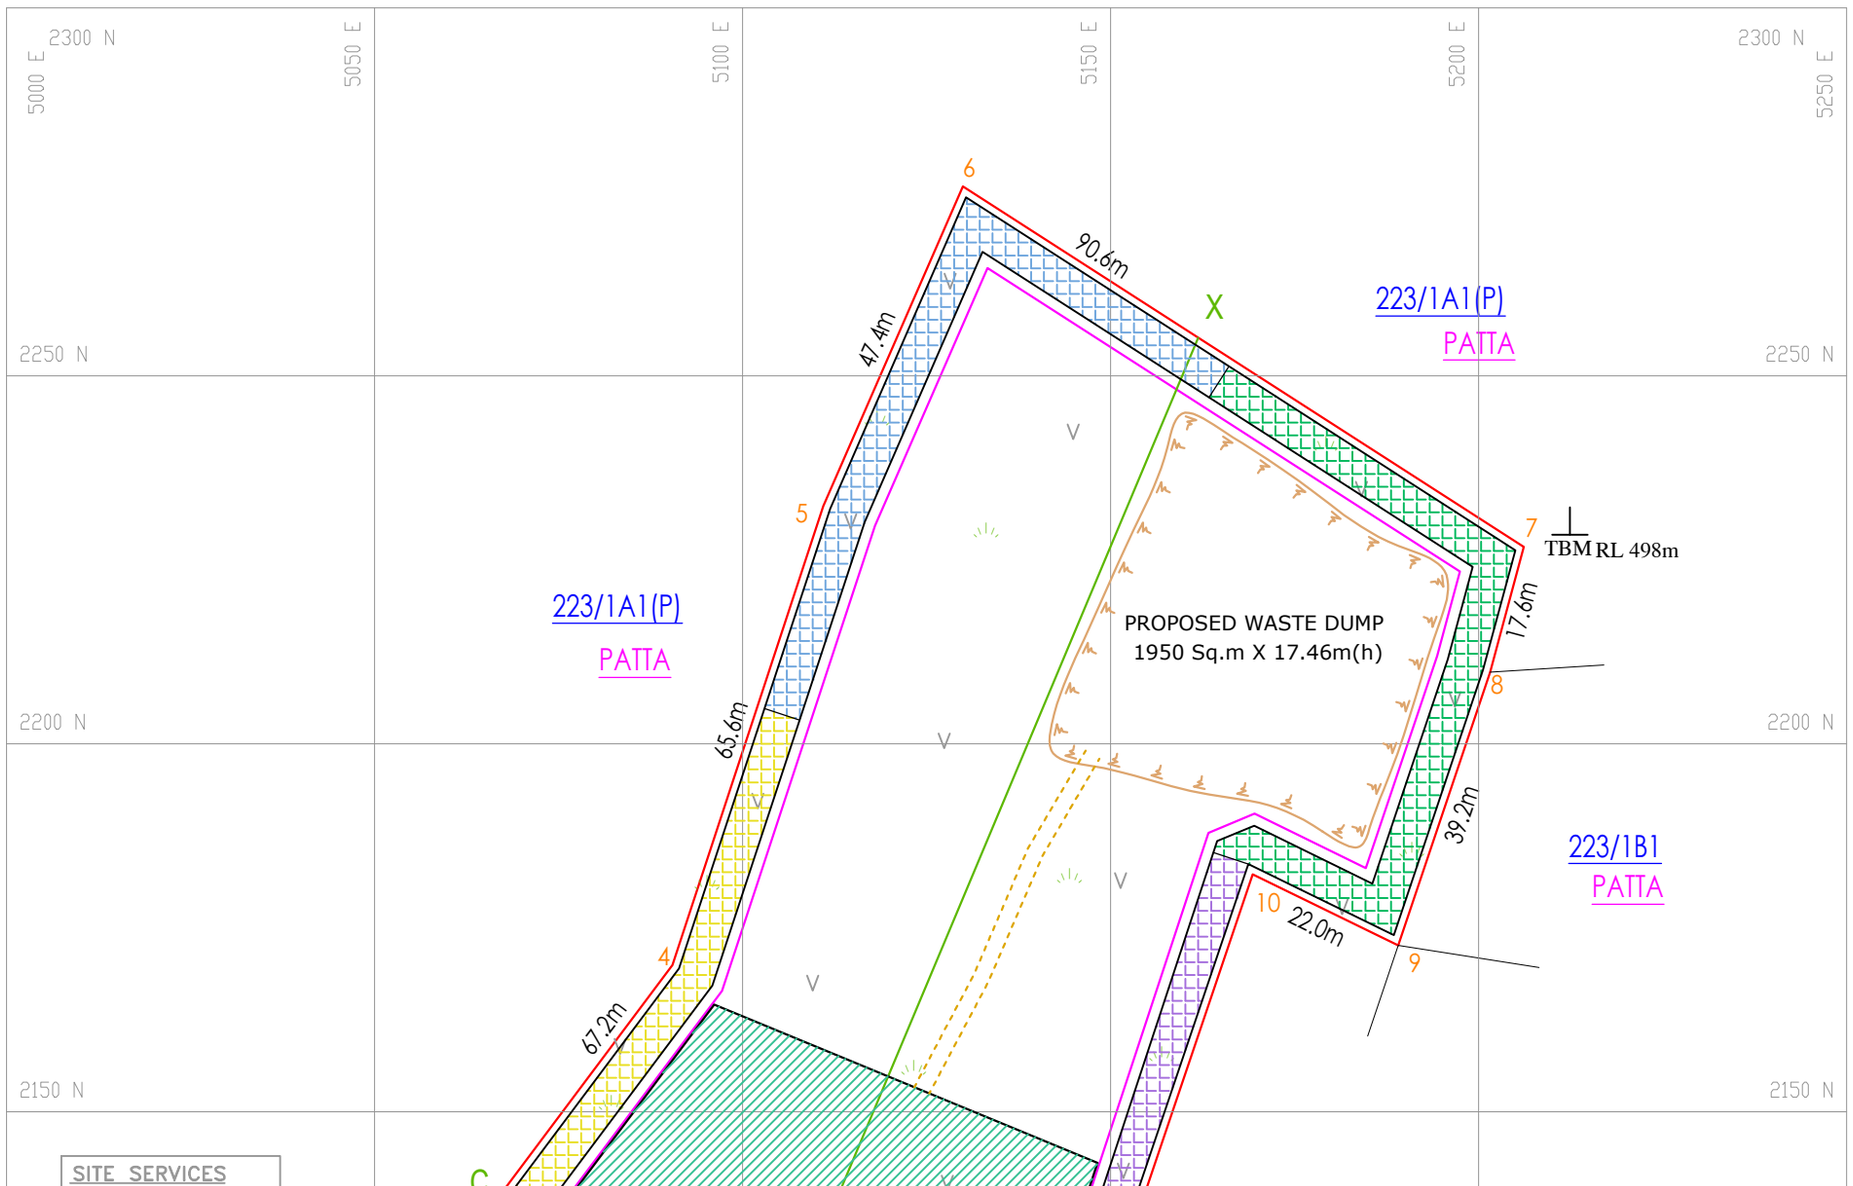

SECTION ALONG X–Y

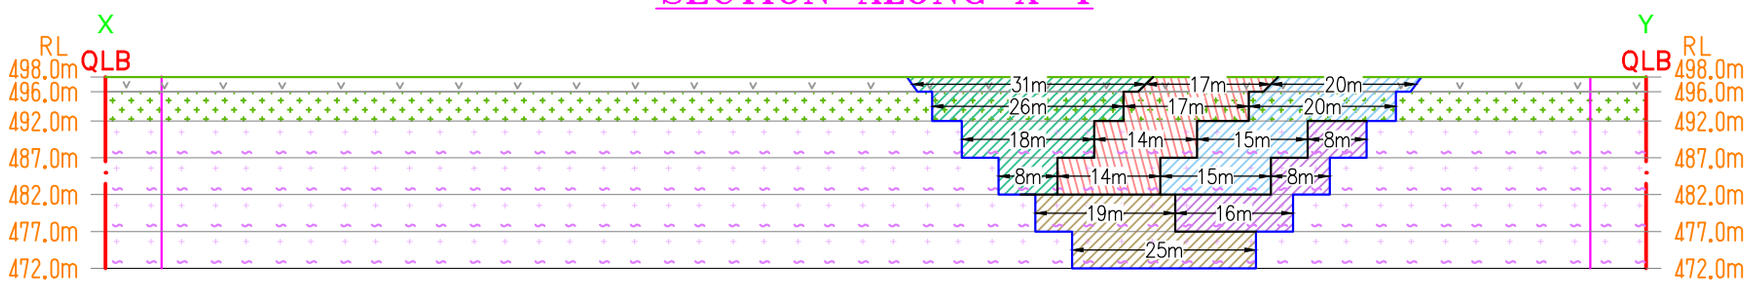

SECTION ALONG C–D

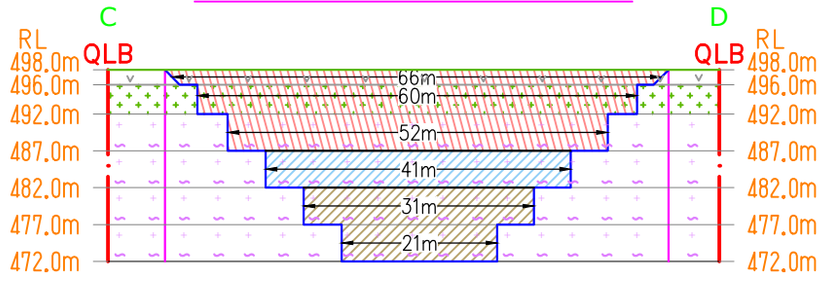

I - yr Proposed area to be Quarried
II - yr Proposed area to be Quarried
III - yr Proposed area to be Quarried
IV - yr Proposed area to be Quarried
V - yr Proposed area to be Quarried

I - yr Proposed area to be Planted
II - yr Proposed area to be Planted
III - yr Proposed area to be Planted
IV - yr Proposed area to be Planted
V - yr Proposed area to be Planted

PLATE NO.V

DATE OF SURVEY:16.03.2026

APPLICANT:

M/s.AB GRANITE
223/1A,CHENDRAPALLI VILLAGE,
ANCHUR POST,
BARGUR TALUK,
KRISHNAGIRI-635 203.

LOCATION OF QUARRY LEASE APPLIED AREA:

SF.NOS :223/1A1(P)&224/2A(P),
EXTENT :1.80.00 HA,
VILLAGE :CHENDRAPALLI,
TALUK :BARGUR,
DISTRICT :KRISHNAGIRII,
STATE :TAMILNADU.

INDEX

- Q.L.APPLIED AREA BOUNDARY
- 7.5m SAFETY DISTANCE
- TEMPORARY BENCH MARK
- TOP SOIL
- WEATHERED ROCK
- STRIKE AND DIP
- GREY GRANITE
- SCRUB
- APPROACH ROAD
- QUARRY HAUL ROAD
- DUMP

YEARWISE DEVELOPMENT AND PRODUCTION PLAN & SECTIONS

SCALE 1:1000

PREPARED BY:

THIS IS TO CERTIFY THAT THE INFORMATION IN THIS PLATE IS TRUE AND CORRECT TO THE BEST OF MY KNOWLEDGE BASED UPON THE LEASEMAP AUTHENTICATED BY STATE GOVERNMENT

B.VENGADAGIRI,M.Sc.,
QUALIFIED PERSON
Under Rule 15(I)(a)and(b)of MCR,2016

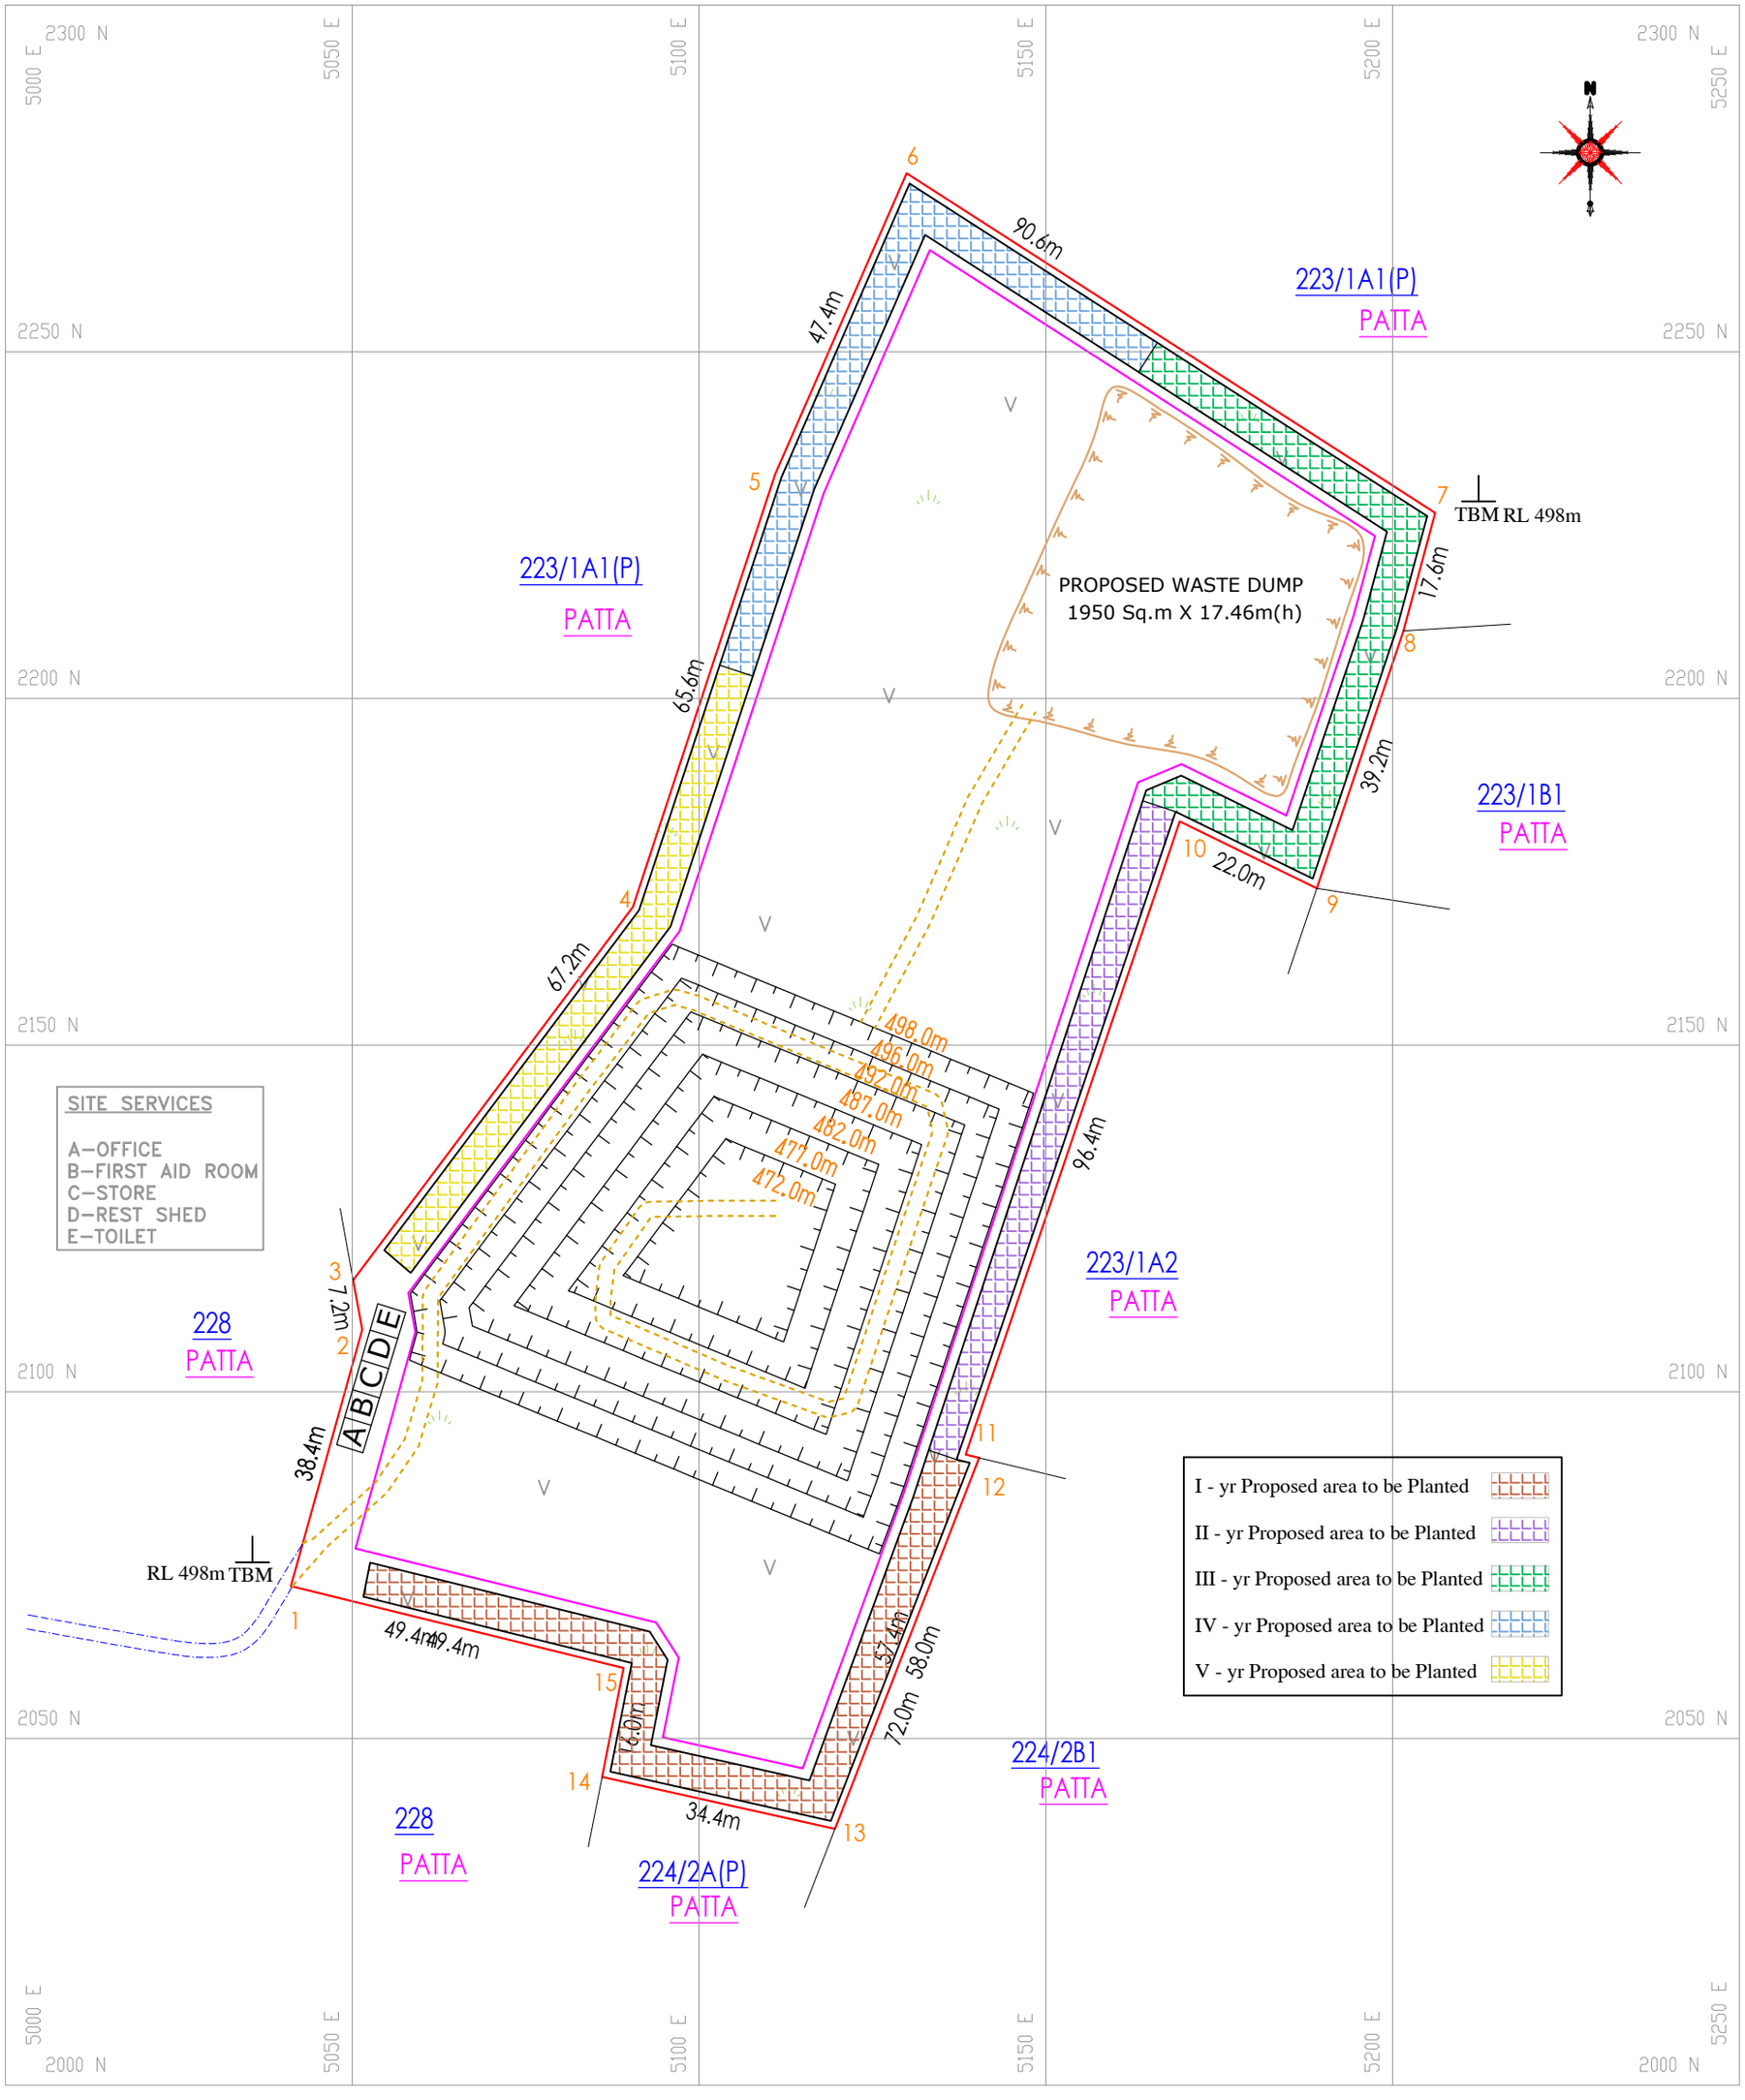


PLATE NO.VI

DATE OF SURVEY:16.03.2026

APPLICANT:

M/s.AB GRANITE
223/1A,CHENDRAPALLI VILLAGE,
ANCHUR POST,
BARGUR TALUK,
KRISHNAGIRI-635 203.

LOCATION OF QUARRY LEASE APPLIED AREA:

SF.NOS :223/1A1(P)&224/2A(P),
EXTENT :1.80.00 HA,
VILLAGE :CHENDRAPALLI,
TALUK :BARGUR,
DISTRICT :KRISHNAGIRII,
STATE :TAMILNADU.

INDEX

- Q.L.APPLIED AREA BOUNDARY
- 7.5m SAFETY DISTANCE
- TEMPORARY BENCH MARK (TBM)
- TOP SOIL (V V V)
- WEATHERED ROCK
- STRIKE AND DIP
- GREY GRANITE (+ + +)
- SCRUB
- APPROACH ROAD
- QUARRY HAUL ROAD
- DUMP
- QUARRY PIT

QUARRY LAYOUT AND AFFORESTATION PLAN

SCALE 1:1000

PREPARED BY:

THIS IS TO CERTIFY THAT THE INFORMATION IN THIS PLATE IS TRUE AND CORRECT TO THE BEST OF MY KNOWLEDGE BASED UPON THE LEASEMAP AUTHENTICATED BY STATE GOVERNMENT

B.VENGADAGIRI,M.Sc.,
QUALIFIED PERSON
Under Rule 15(I)(a)and(b)of MCR,2016

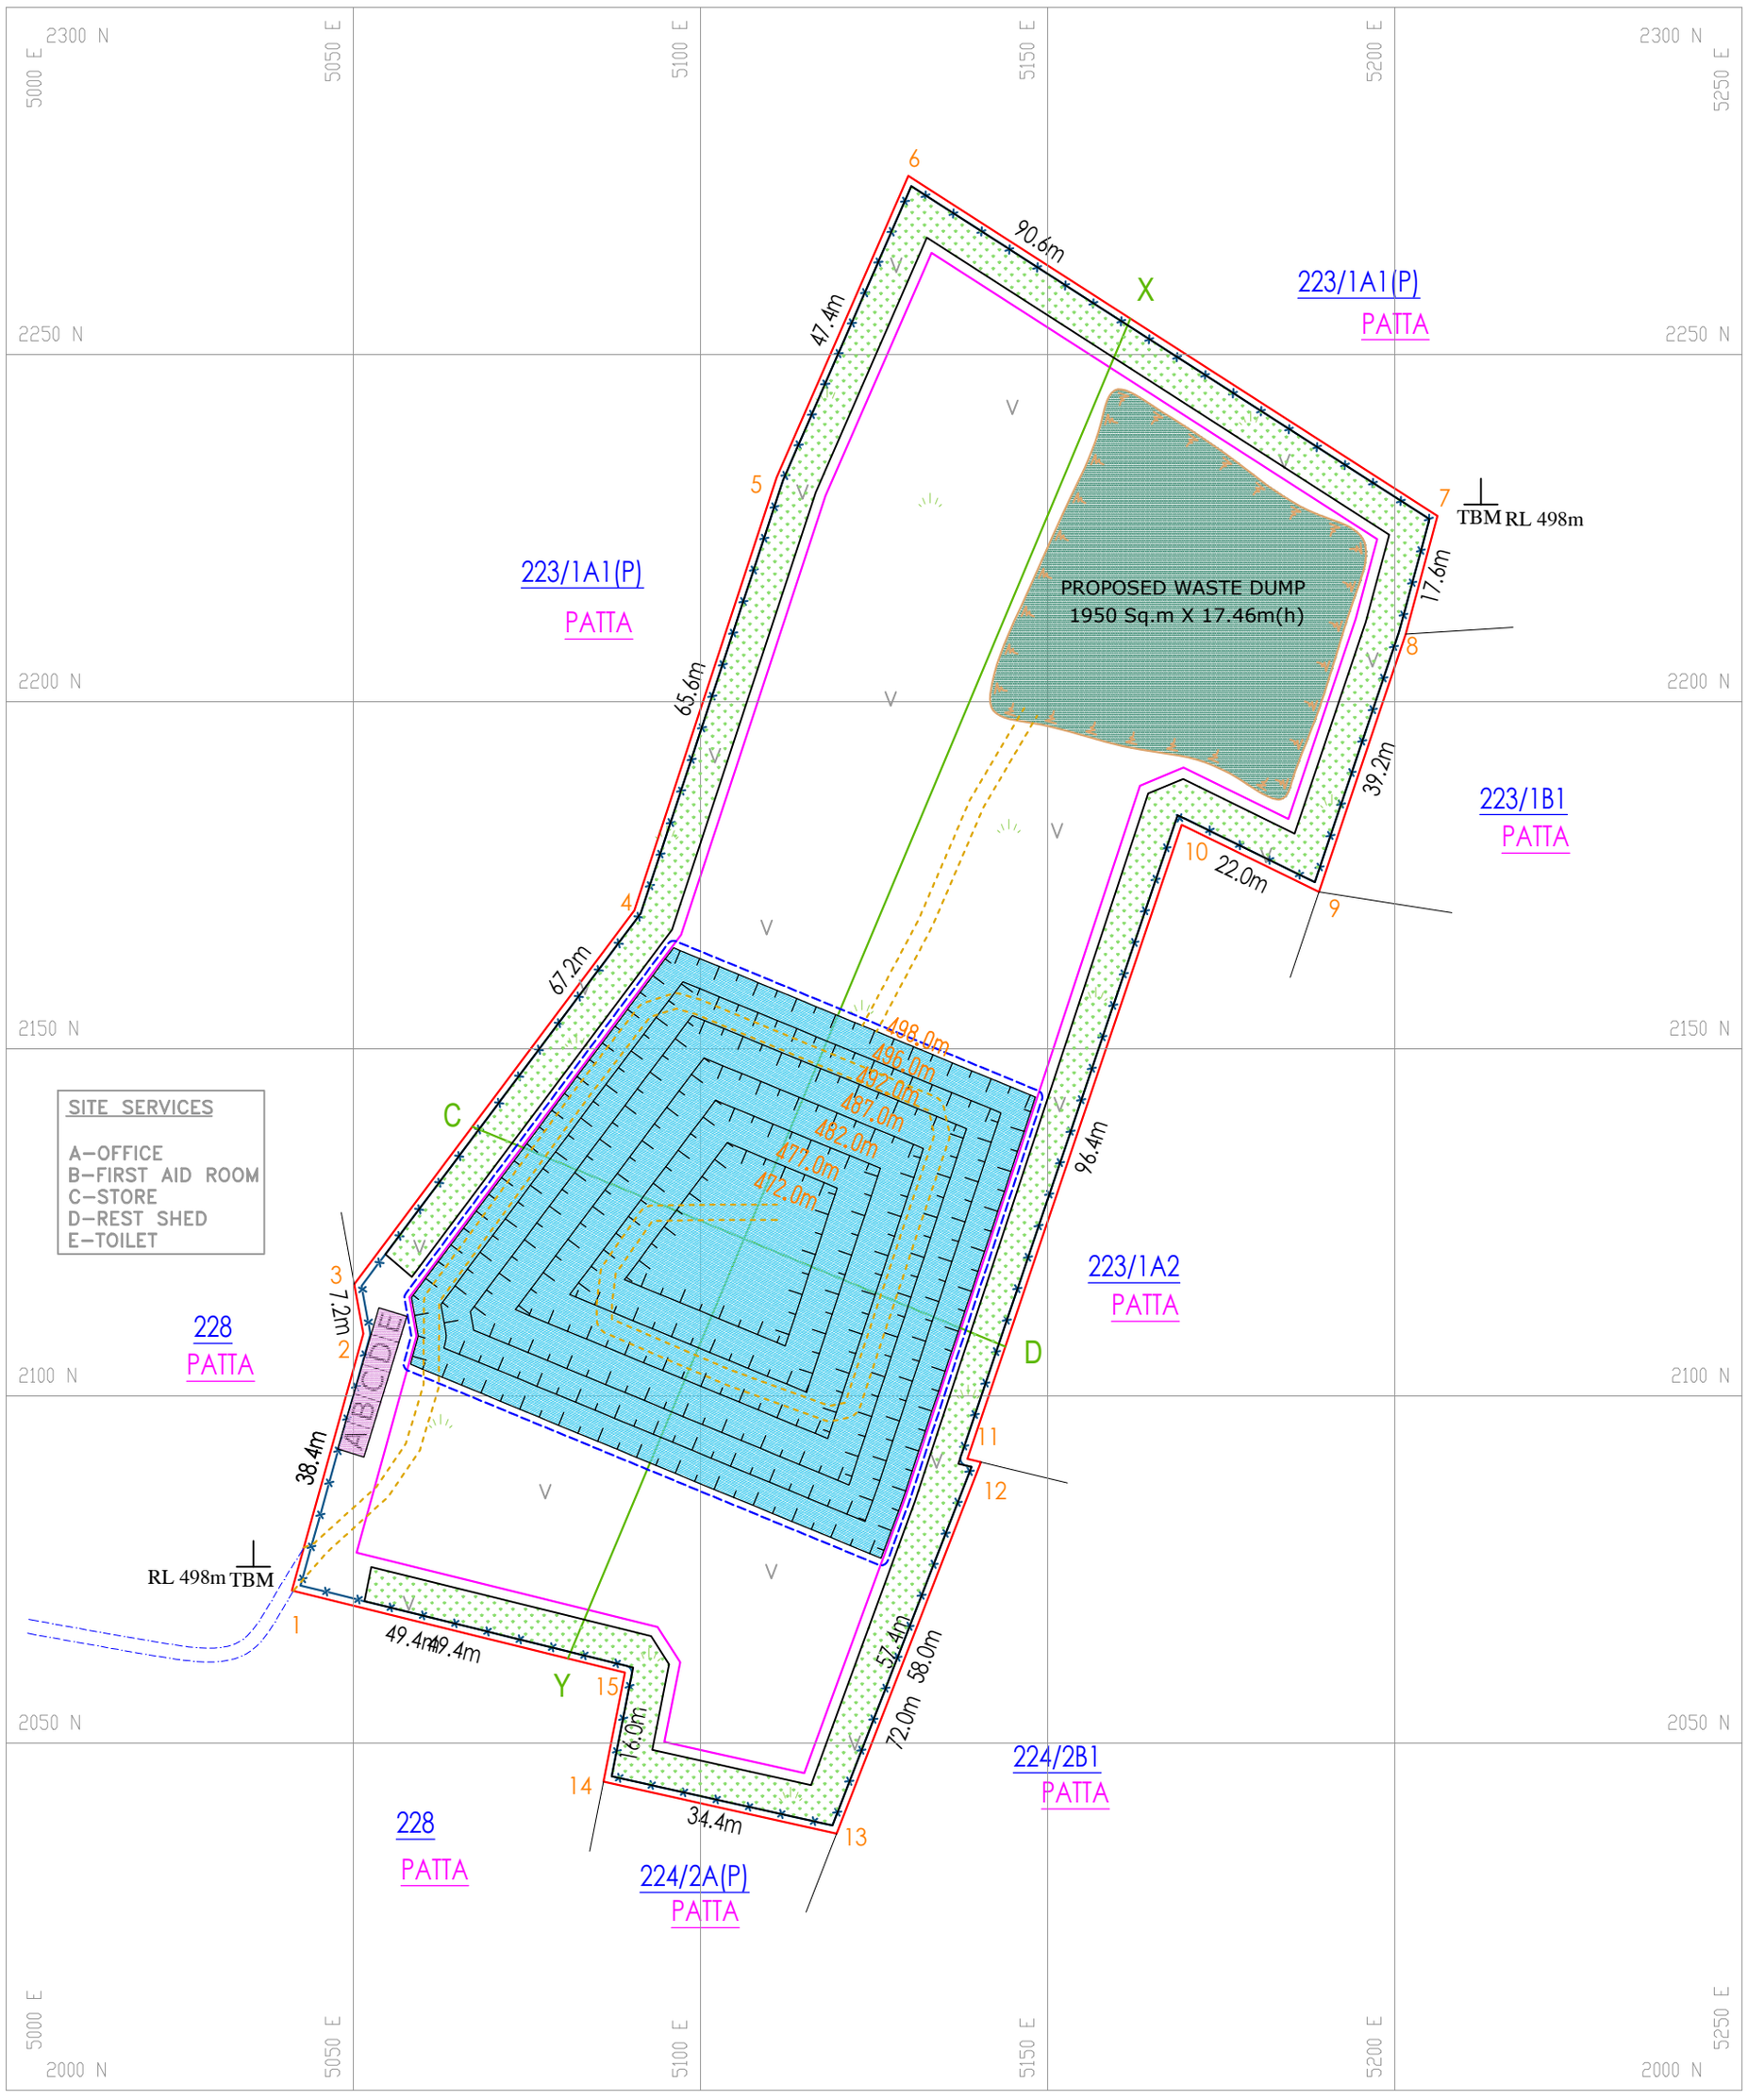


PLATE NO.VII

DATE OF SURVEY:16.03.2026

APPLICANT:

M/s.AB GRANITE
223/1A,CHENDRAPALLI VILLAGE,
ANCHUR POST,
BARGUR TALUK,
KRISHNAGIRI-635 203.


LOCATION OF QUARRY LEASE APPLIED AREA:

SF.NOS :223/1A1(P)&224/2A(P),
EXTENT :1.80.00 HA,
VILLAGE :CHENDRAPALLI,
TALUK :BARGUR,
DISTRICT :KRISHNAGIRII,
STATE :TAMILNADU.

INDEX

- Q.L.APPLIED AREA BOUNDARY
- 7.5m SAFETY DISTANCE
- TEMPORARY BENCH MARK (TBM)
- TOP SOIL (V V V)
- WEATHERED ROCK
- STRIKE AND DIP
- GREY GRANITE
- SCRUB
- APPROACH ROAD
- QUARRY HAUL ROAD
- DUMP
- QUARRY PIT
- FENCING
- PROPOSED GARLAND DRAIN


SECTION ALONG X–Y

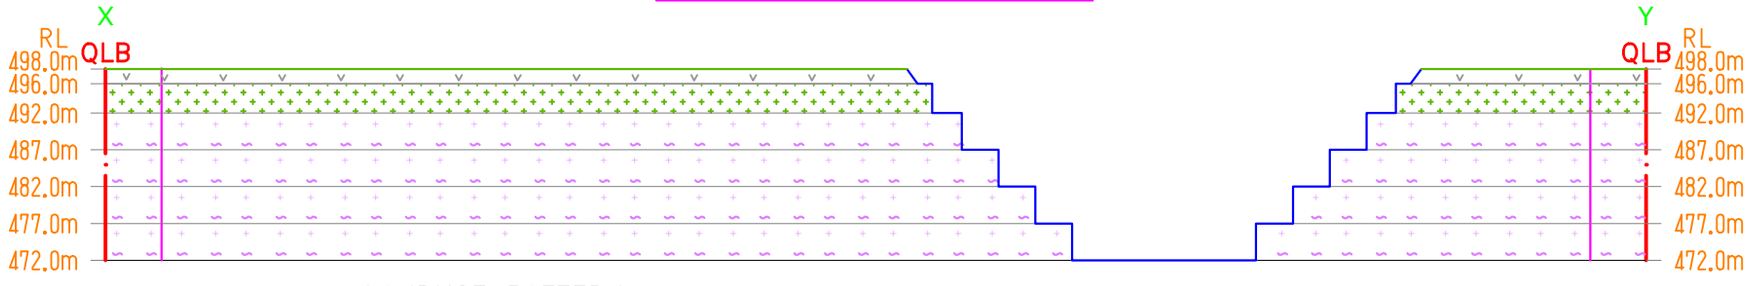

LANDUSE PATTERN

DESCRIPTION	PRESENT AREA(Ha)	AREA TO BE REQUIRED AT THE PRESENT MINING PLAN PERIOD (Ha)	AAT THE END OF LIFE OF QUARRY(Ha)	Color code
AREA UNDER QUARRY	NIL	0.47.13	1.33.93	
DUMPS	NIL	0.19.50	BACK FILLING	
INFRASTRUCTURE	NIL	0.01.00	0.02.00	
ROADS	NIL	0.01.00	0.02.00	
GREEN BELT	NIL	0.28.10	0.28.10	
STICKING BLOCKS	1.80.00	0.83.27	0.13.97	
TOTAL	1.80.00	1.80.00	1.80.00	

SECTION ALONG C–D

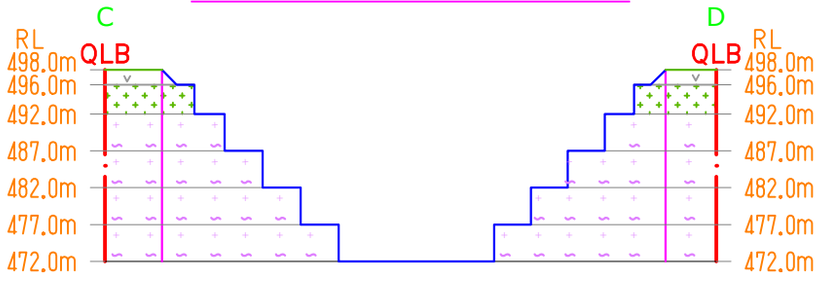


PROGRESSIVE QUARRY CLOSURE PLAN AND SECTIONS

SCALE 1:1000

PREPARED BY:

THIS IS TO CERTIFY THAT THE INFORMATION IN THIS PLATE IS TRUE AND CORRECT TO THE BEST OF MY KNOWLEDGE BASED UPON THE LEASEMAP AUTHENTICATED BY STATE GOVERNMENT

B.VENGADAGIRI,M.Sc.,
QUALIFIED PERSON
Under Rule 15(1)(a)and(b)of MCR,2016

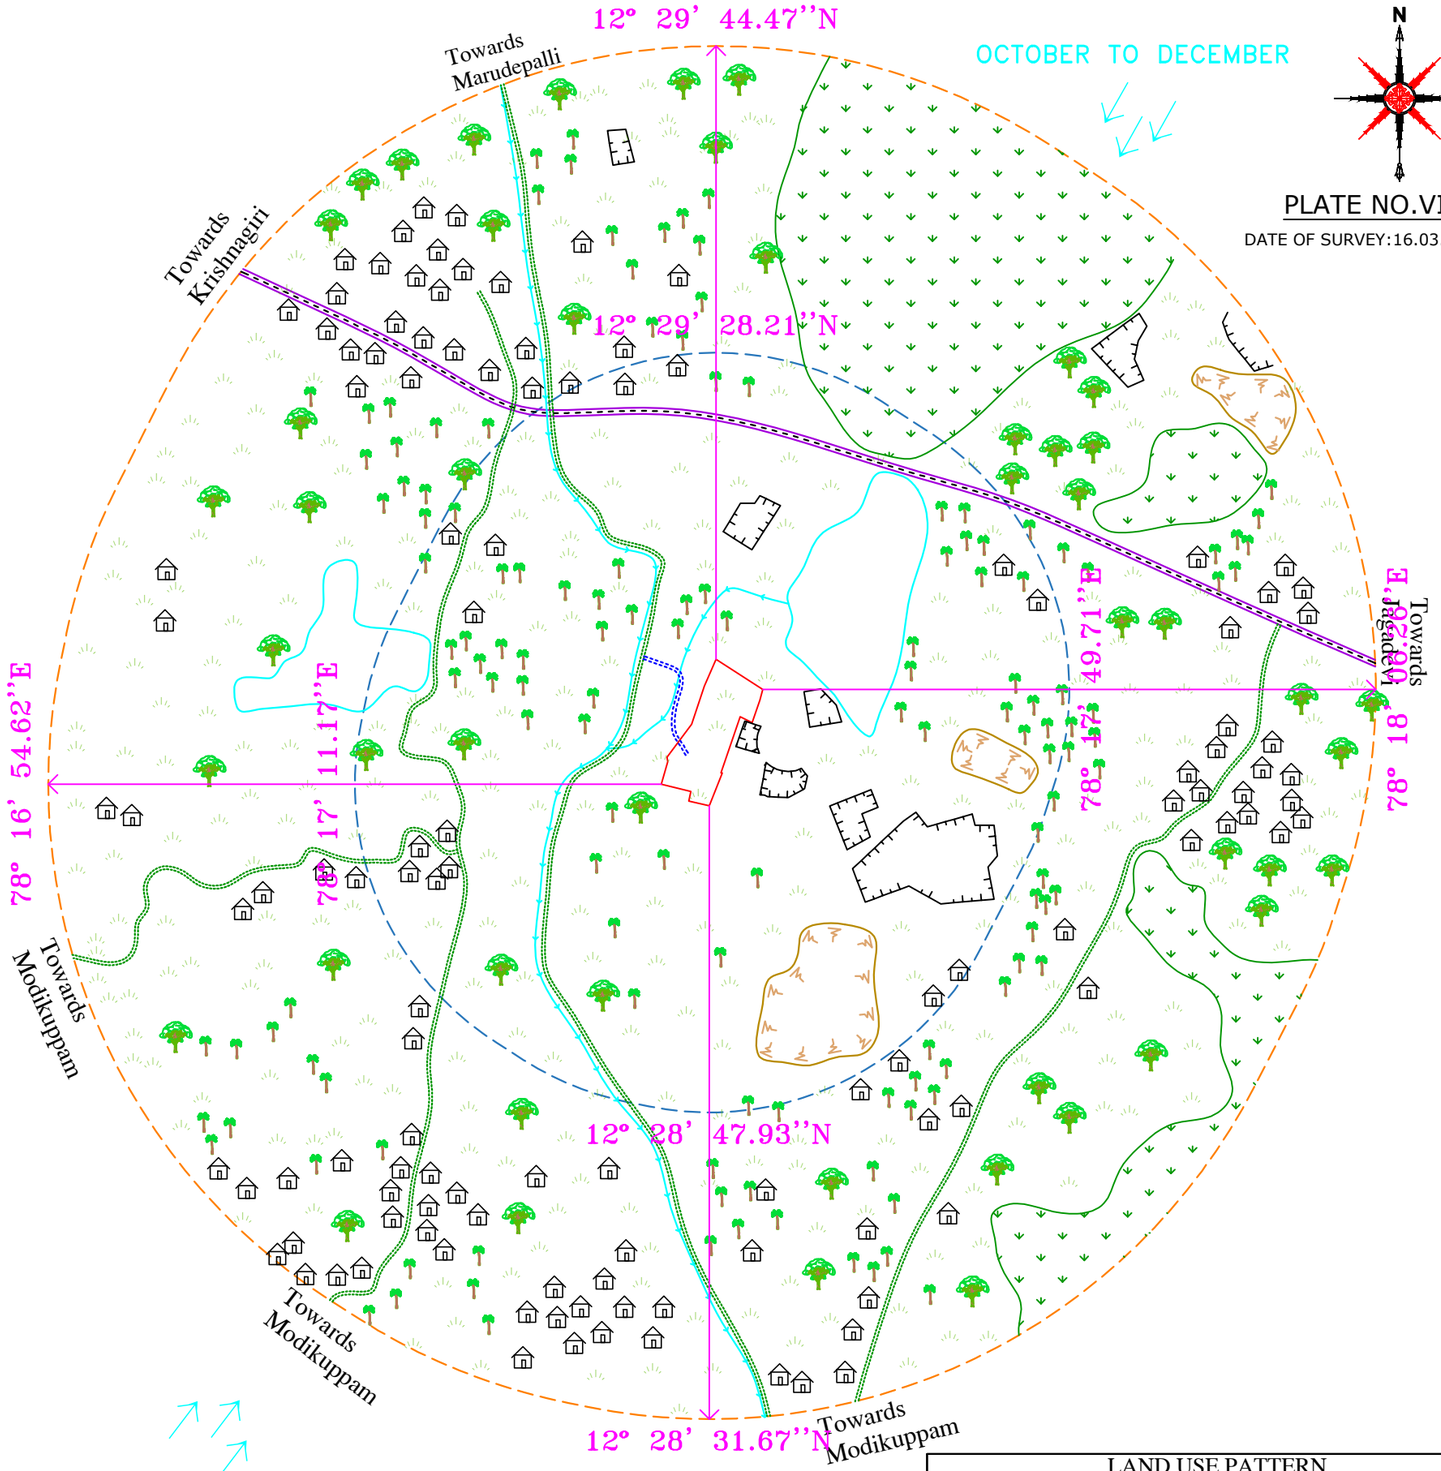

LAND USE PATTERN	
DESCRIPTION	PERCENTAGE
ROADS	(10%)
HABITATION	(10%)
SEASONAL AGRICULTURAL LAND	(55%)
TREES	(10%)
HILL LOCK AREA	(15%)
TOTAL	100%

APPLICANT:

M/s.AB GRANITE
223/1A,CHENDRAPALLI VILLAGE,
ANCHUR POST,
BARGUR TALUK,
KRISHNAGIRI-635 203.

LOCATION OF QUARRY LEASE APPLIED AREA:

SF.NOS	:223/1A1(P)&224/2A(P),
EXTENT	:1.80.00 HA,
VILLAGE	:CHENDRAPALLI,
TALUK	:BARGUR,
DISTRICT	:KRISHNAGIRII,
STATE	:TAMILNADU.

TOPO SHEET NO. : 57 L/07

LATITUDE : 12° 29' 04.19''N to 12° 29' 11.96''N

LONGITUDE : 78° 17' 27.71''E to 78° 17' 33.17''E

INDEX

- Q.LEASE BOUNDARY
- 1KM RADIUS
- 500m RADIUS
- WIND DIRECTION
- TREES
- NATIONAL HIGHWAY–66
- PANCHAYAT ROAD
- APPROACH ROAD
- AGRICULTURAL LAND
- HABITATION
- HILLLOCK
- QUARRY PIT
- ERI
- DUMP
- ODAI


ENVIRONMENTAL AND LANDUSE PLAN FOR 1Km RADIUS

SCALE 1:10000

PREPARED BY:

THIS IS TO CERTIFY THAT THE INFORMATION IN THIS PLATE IS TRUE AND CORRECT TO THE BEST OF MY KNOWLEDGE BASED UPON THE LEASEMAP AUTHENTICATED BY STATE GOVERNMENT

B.VENGADAGIRI,M.Sc.,
QUALIFIED PERSON
Under Rule 15(1)(a)and(b)of MCR,2016

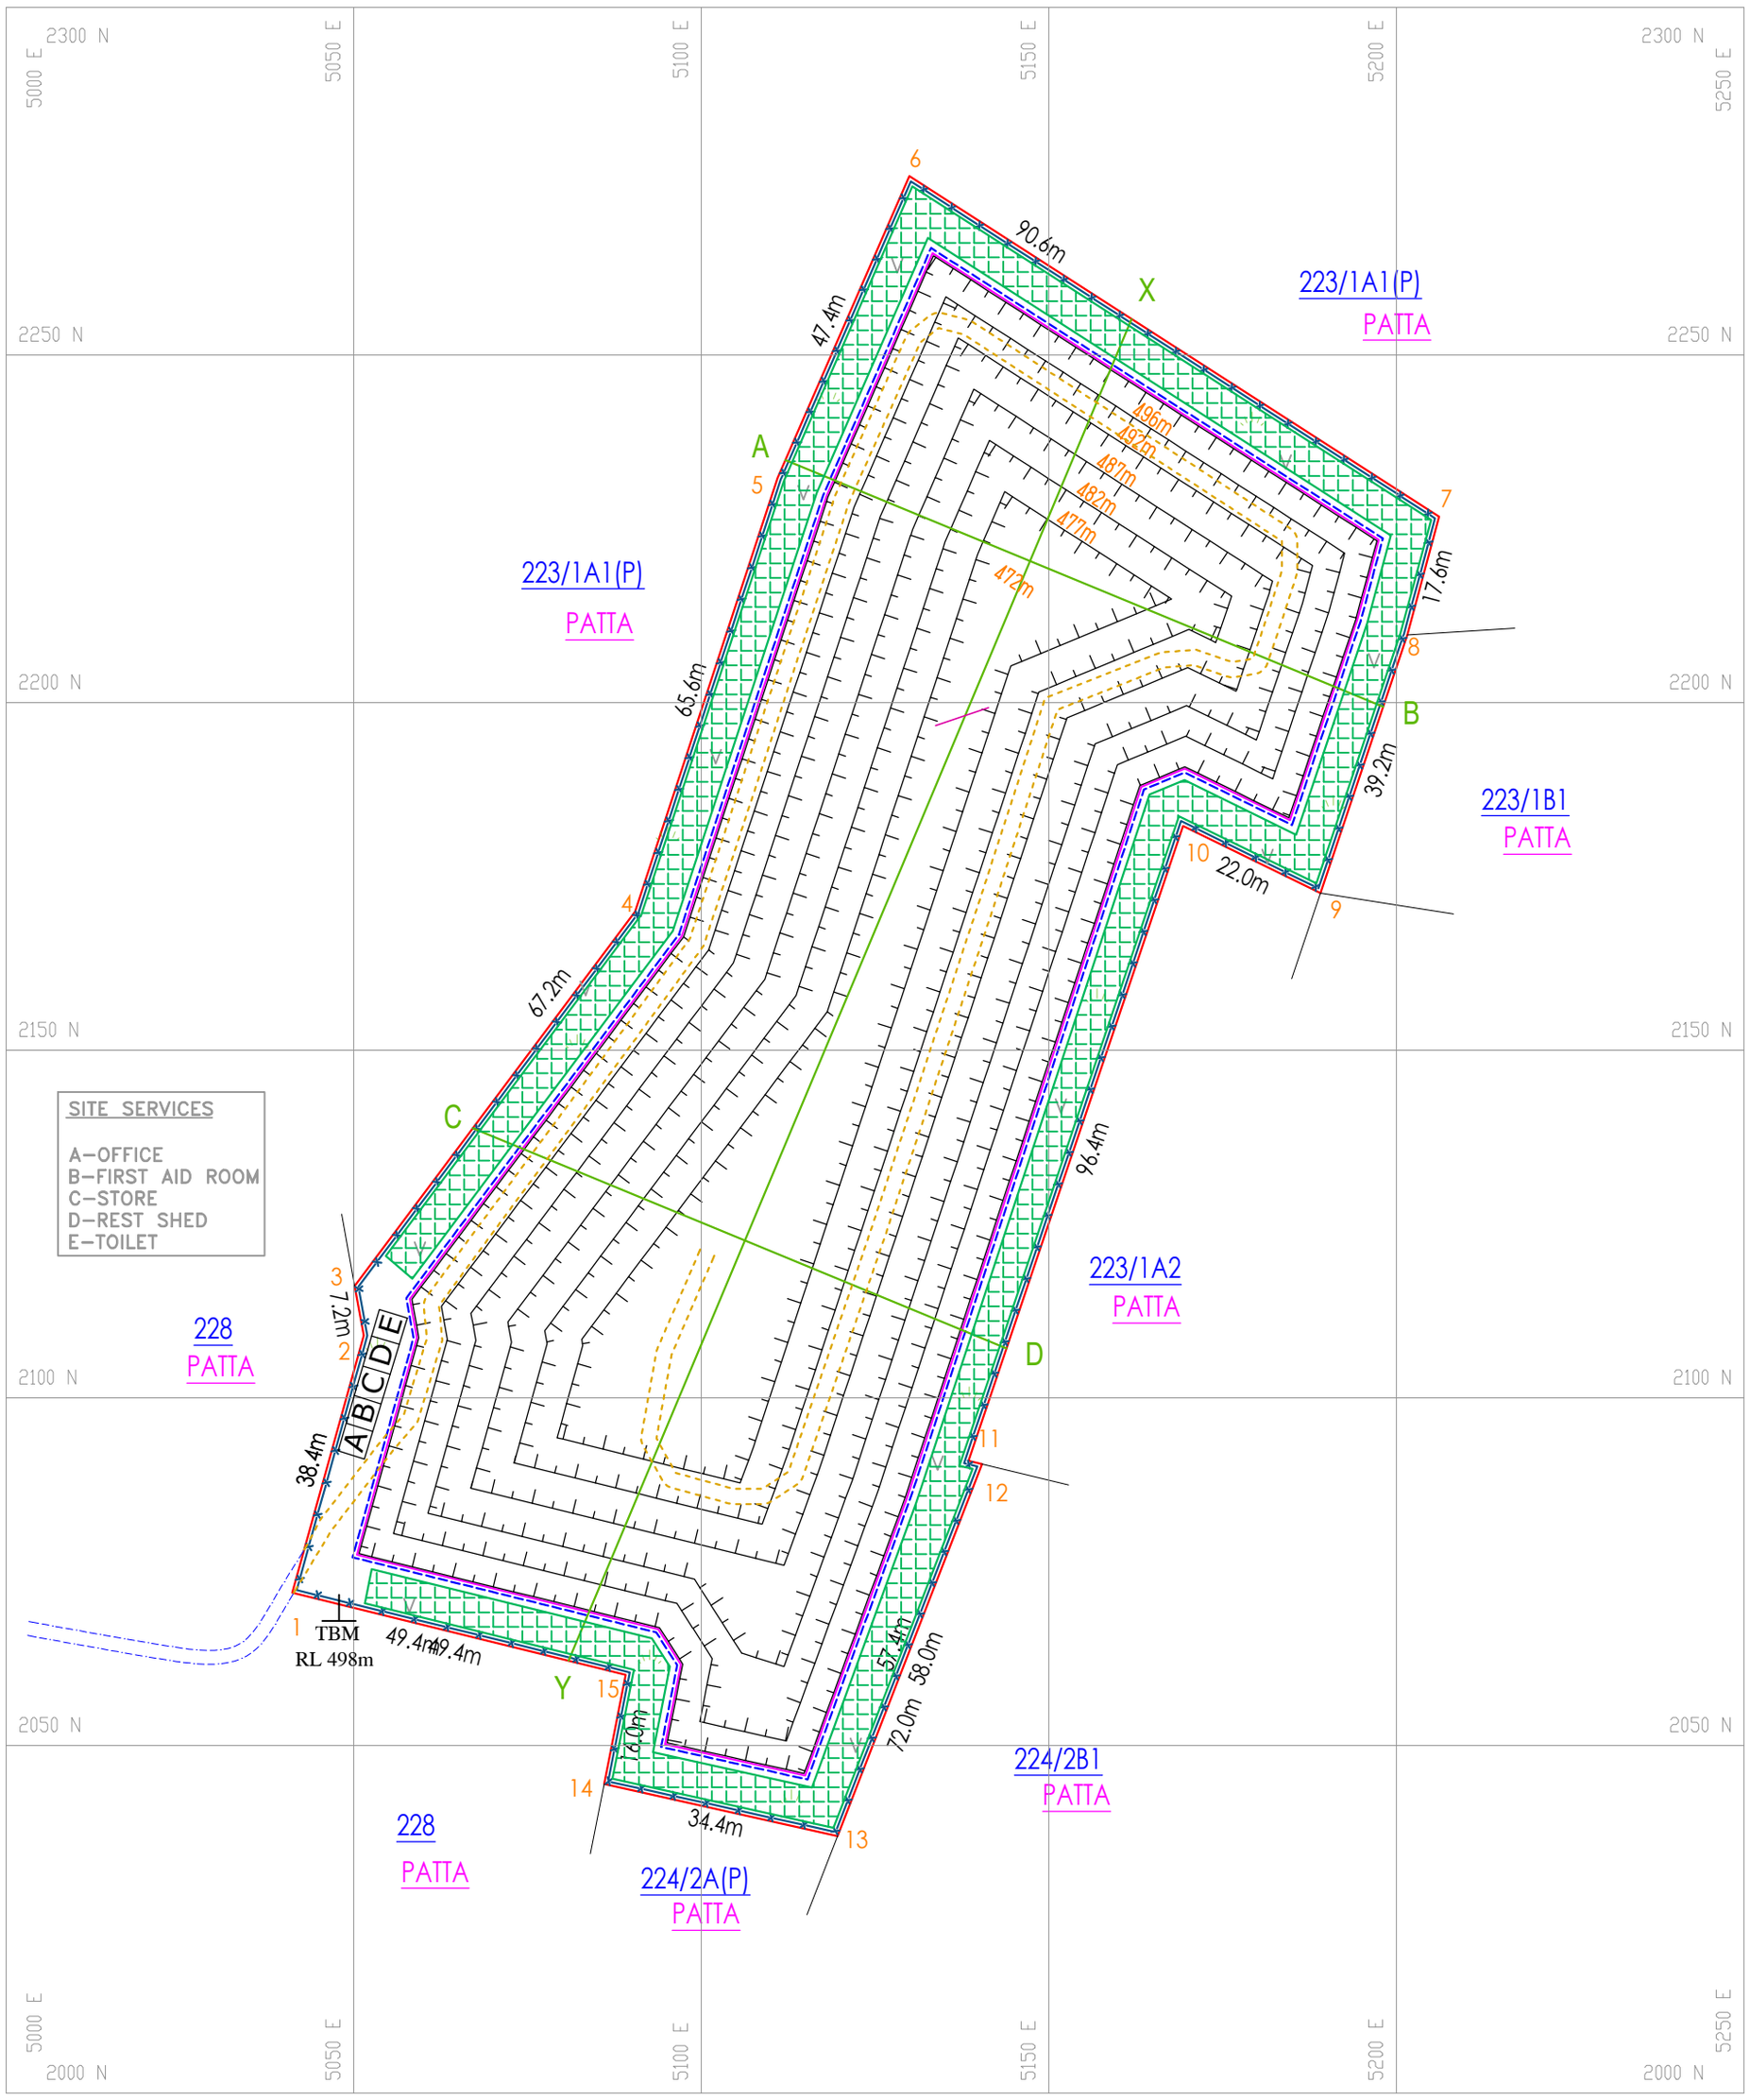

SITE SERVICES

A–OFFICE
B–FIRST AID ROOM
C–STORE
D–REST SHED
E–TOILET

ULTIMATE PIT DIMENSION (MAX)
XY-AB= 54mX76m26m(d)
XY-CD= 139mX66mX26m(d)

PLATE NO.IX

DATE OF SURVEY:16.03.2026

APPLICANT:

M/s.AB GRANITE
223/1A,CHENDRAPALLI VILLAGE,
ANCHUR POST,
BARGUR TALUK,
KRISHNAGIRI-635 203.


LOCATION OF QUARRY LEASE APPLIED AREA:

SF.NOS :223/1A1(P)&224/2A(P),
EXTENT :1.80.00 HA,
VILLAGE :CHENDRAPALLI,
TALUK :BARGUR,
DISTRICT :KRISHNAGIRII,
STATE :TAMILNADU.


INDEX

- Q.L.APPLIED AREA BOUNDARY
- 7.5m SAFETY DISTANCE
- TEMPORARY BENCH MARK
- TOP SOIL
- WEATHERED ROCK
- STRIKE AND DIP
- GREY GRANITE
- SCRUB
- APPROACH ROAD
- QUARRY HAUL ROAD
- QUARRY PIT
- PROPOSED BACKFILLING
- BARBED WIRE FENCING
- PROPOSED GARLAND DRAIN
- PLANTATION


SECTION ALONG X–Y

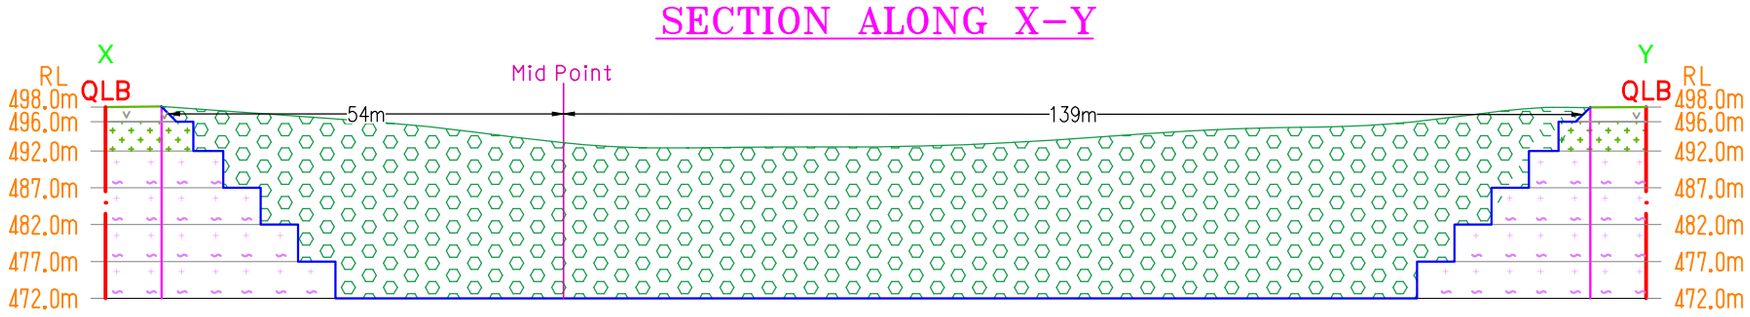

SECTION ALONG A–B

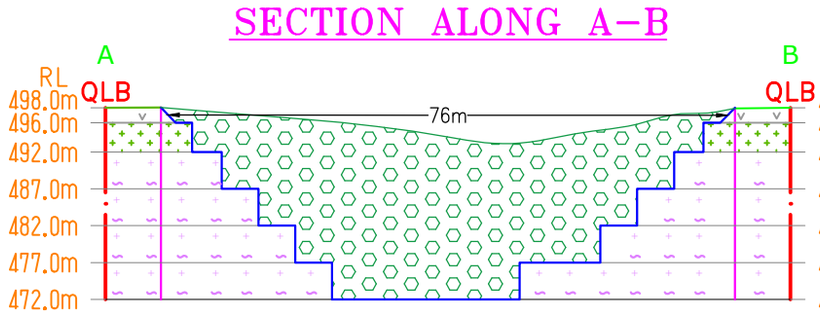

SECTION ALONG C–D

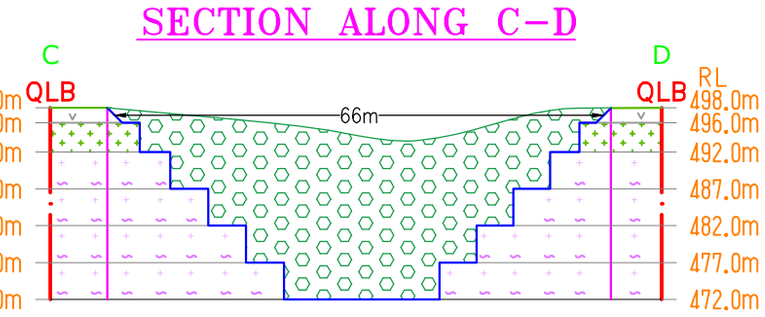

CONCEPTUAL PLAN & SECTIONS

SCALE 1:1000

PREPARED BY:

THIS IS TO CERTIFY THAT THE INFORMATION IN THIS PLATE IS TRUE AND CORRECT TO THE BEST OF MY KNOWLEDGE BASED UPON THE LEASEMAP AUTHENTICATED BY STATE GOVERNMENT

B.VENGADAGIRI,M.Sc.,
QUALIFIED PERSON
Under Rule 15(1)(a)and(b)of MCR,2016